


NOAH TAYLOR
TURF PORTFOLIO

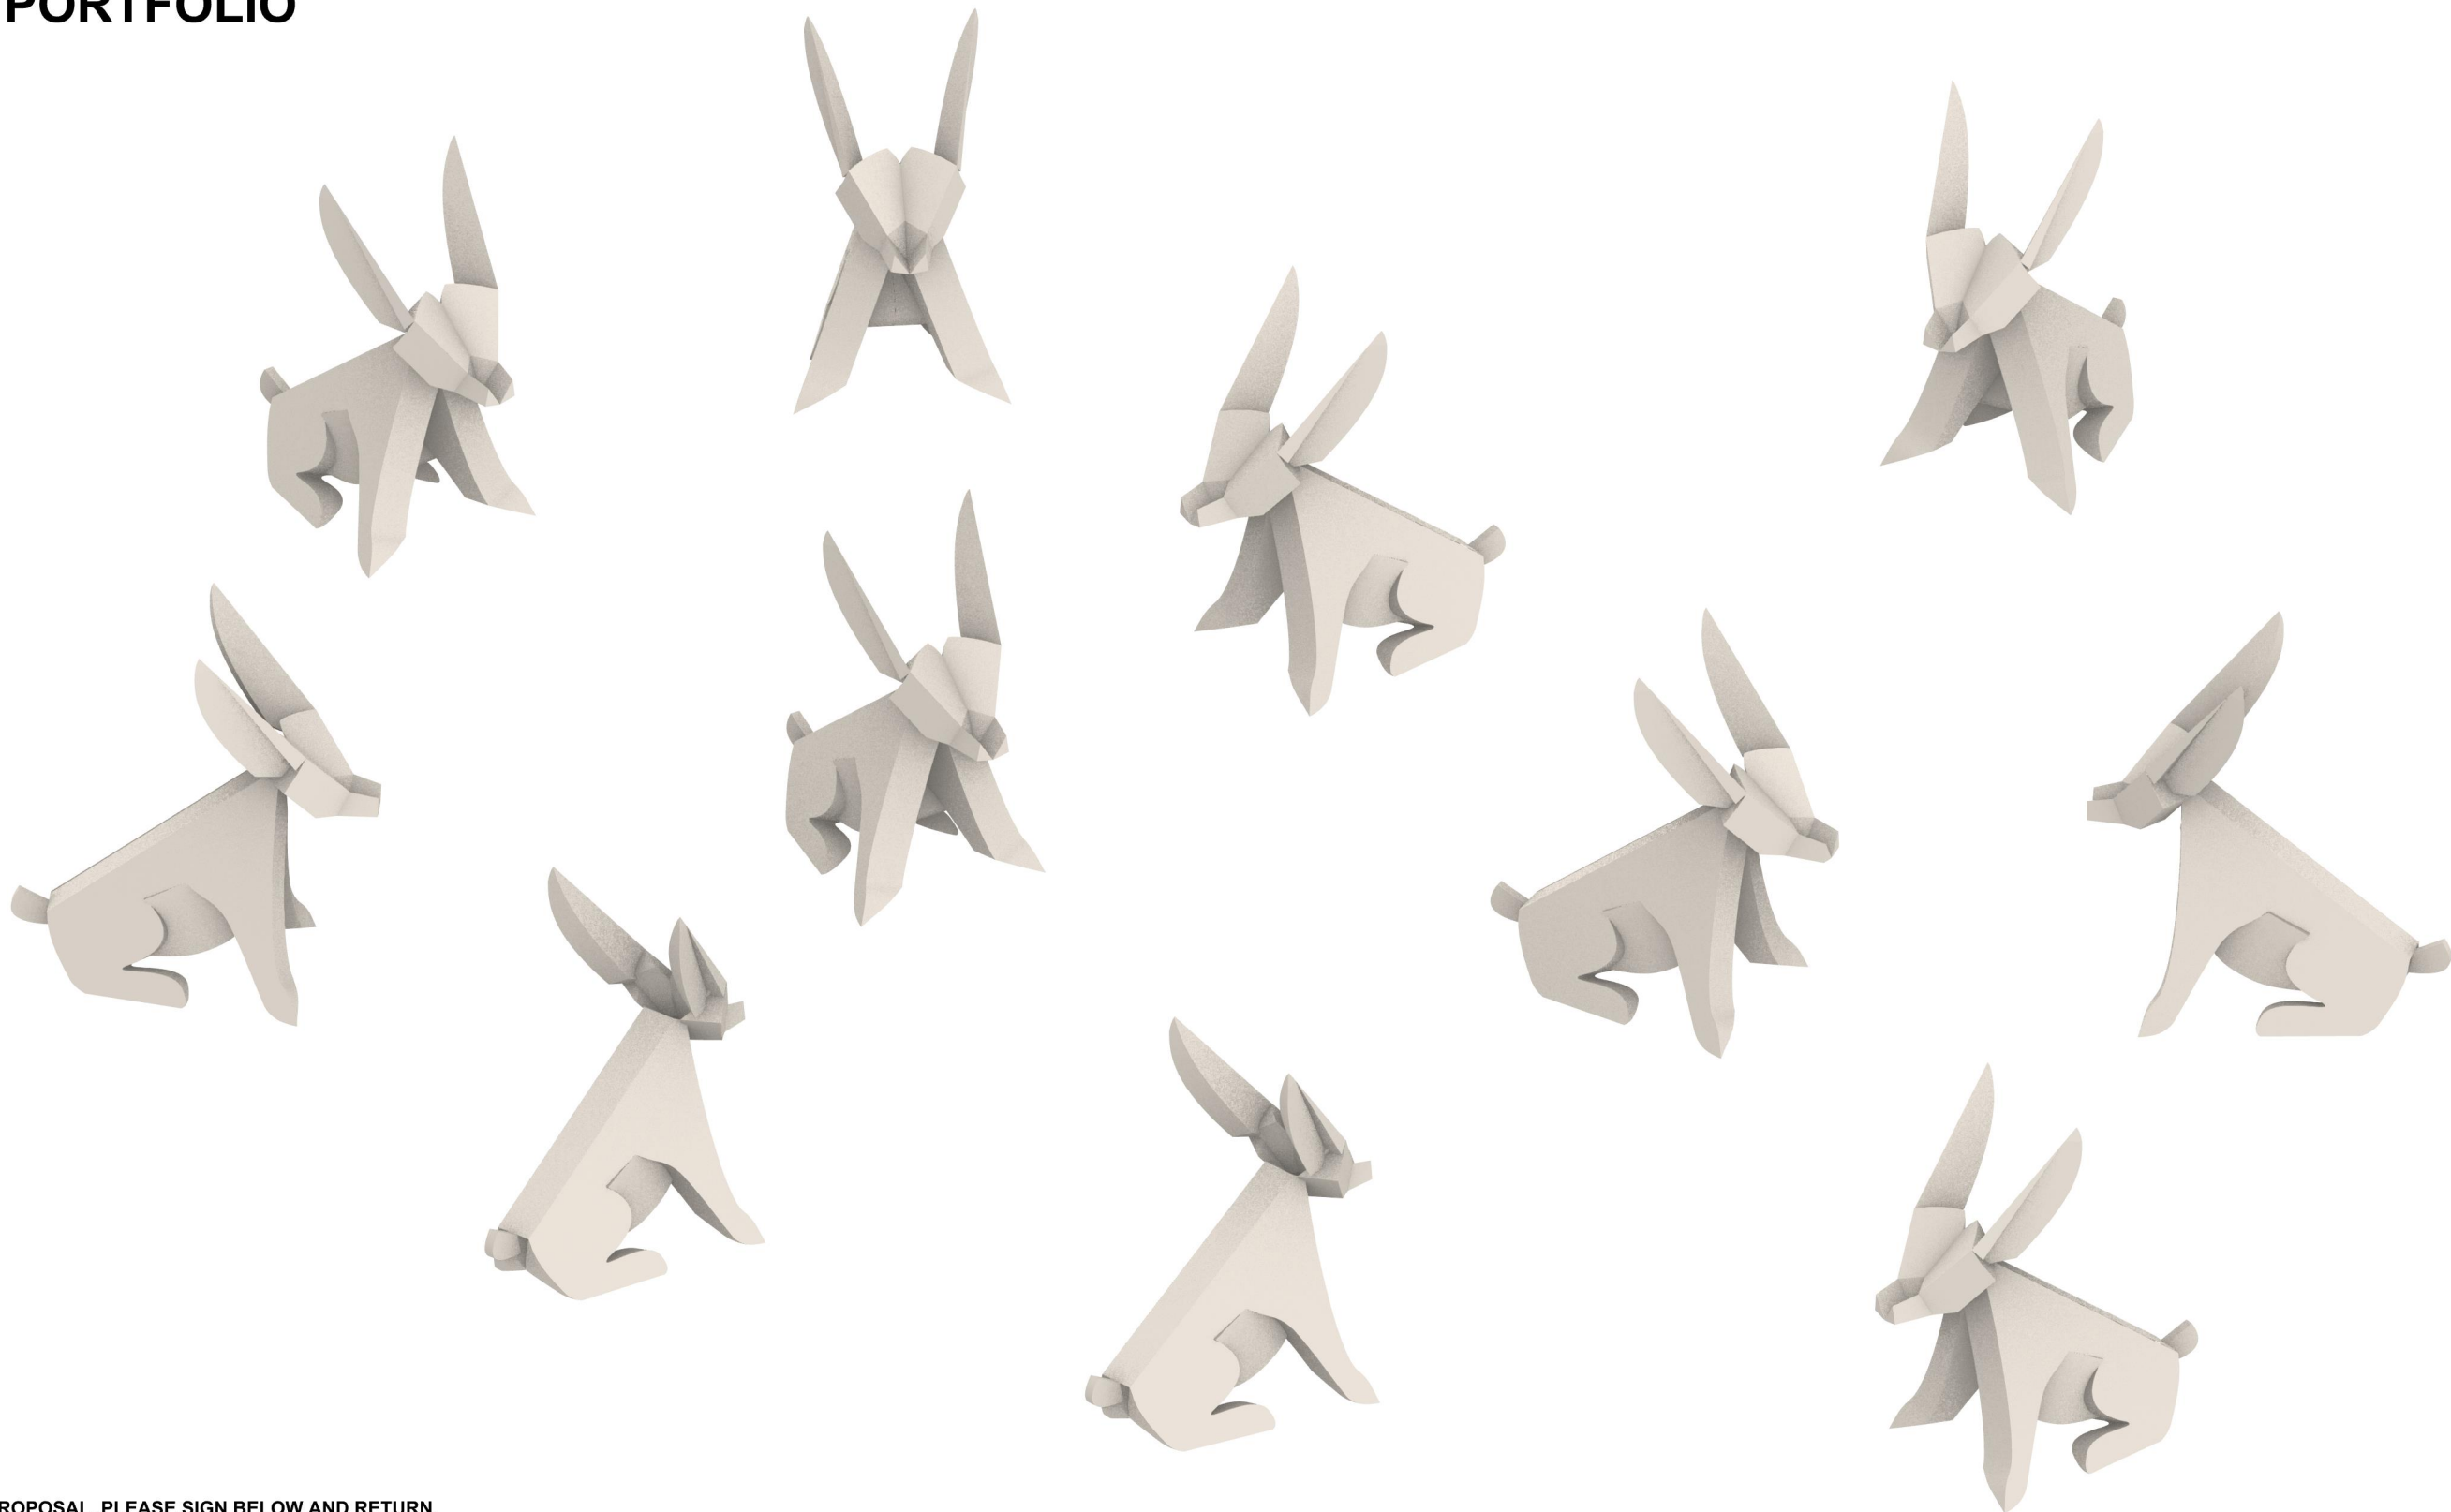

TO APPROVE PROPOSAL, PLEASE SIGN BELOW AND RETURN.





NAME _____

DATE _____

To PD:

Over two years on the design team, my curiosity has always extended beyond shop drawings, finding new ways to build the turf user experience. I came to Turf as a product designer first, and an architectural designer second, and that still rings true. Whether it's a new product that gives a client more versatile options in the field, or a script that helps designers automate daily tasks, my passion comes from finding and filling needs that streamline our outputs at all stages. I would be a good fit for PD because my background in traditional product design has creativity alongside engineering. My experience in computational design also allows me to develop a Turf product as a scripted system from its conception, helping smooth handoffs to Compfab or quick deployments to design. Joining the PD team has always been a goal of mine and I would be thrilled to work with you.


-Noah

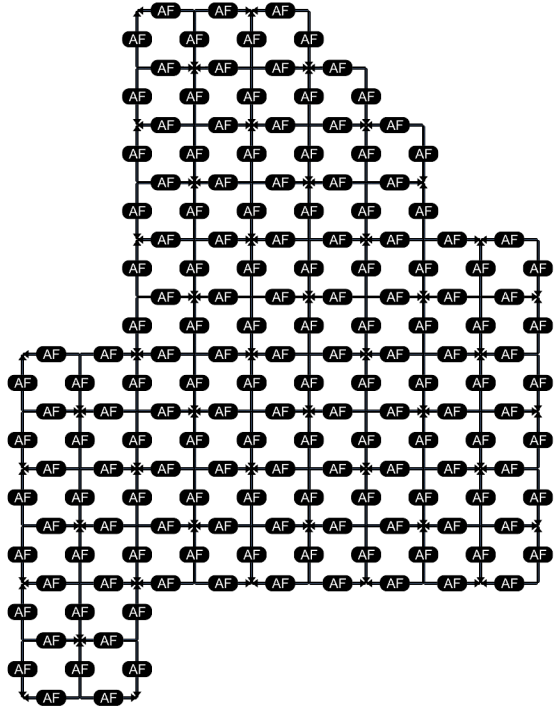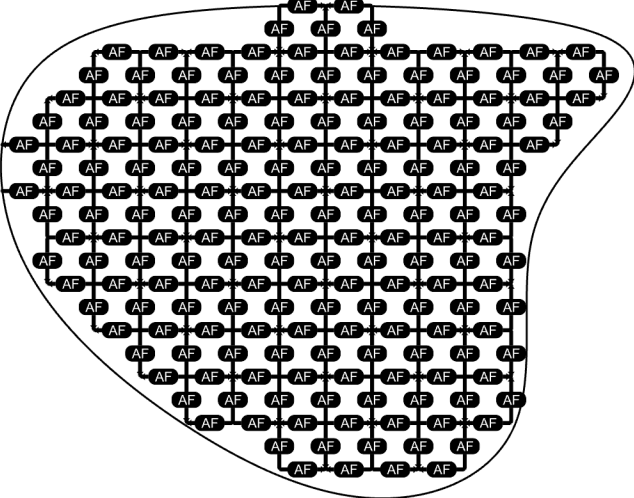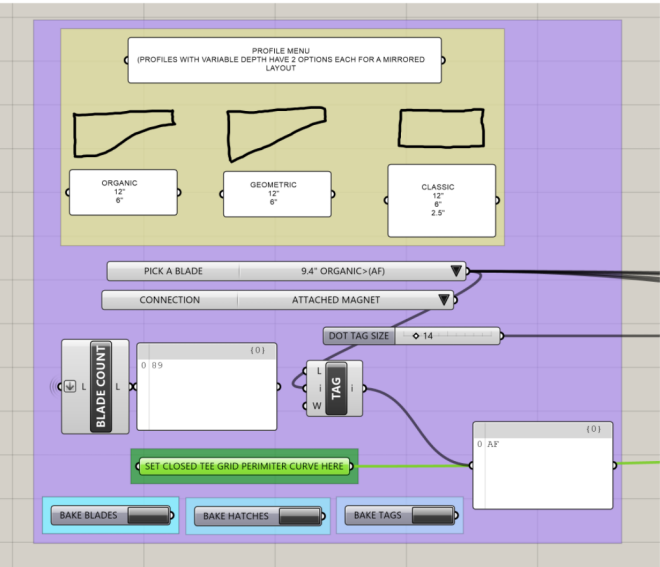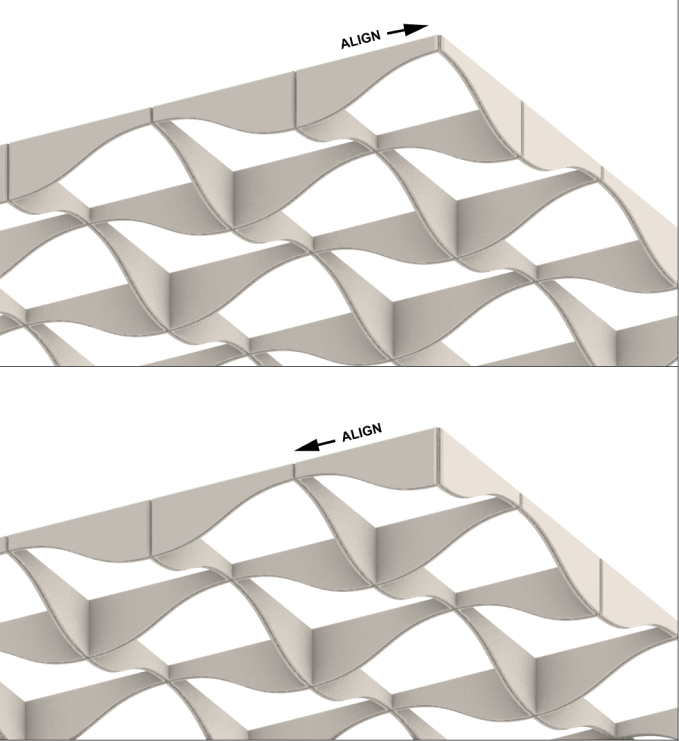			
The Switchblade tool is a powerful way to orient the standard product within spaces. The script finds the minimum distance from a tee grid perimeter where a grid of typical 24" baffles can sit.	The tool is also capable of creating grids in organic shaped spaces, approximating how to best fit the layout of 24" typical baffles based on space limits.	The dashboard of the script allows the designer to set the perimeter curve and profile type from the standard products. The script provides a live count of generated baffles to make scheduling easier. Outputs are massing, tags, and alignment hatches, all bakeable separately	The script has advanced capability for baffles with shallow and deep points. It will auto-align all baffles to create smooth transitions at every point on the grid. directional alignment can be flipped in the tool dashboard,

PARAMETRIC TOOL, SWITCHBLADE


01

NTS

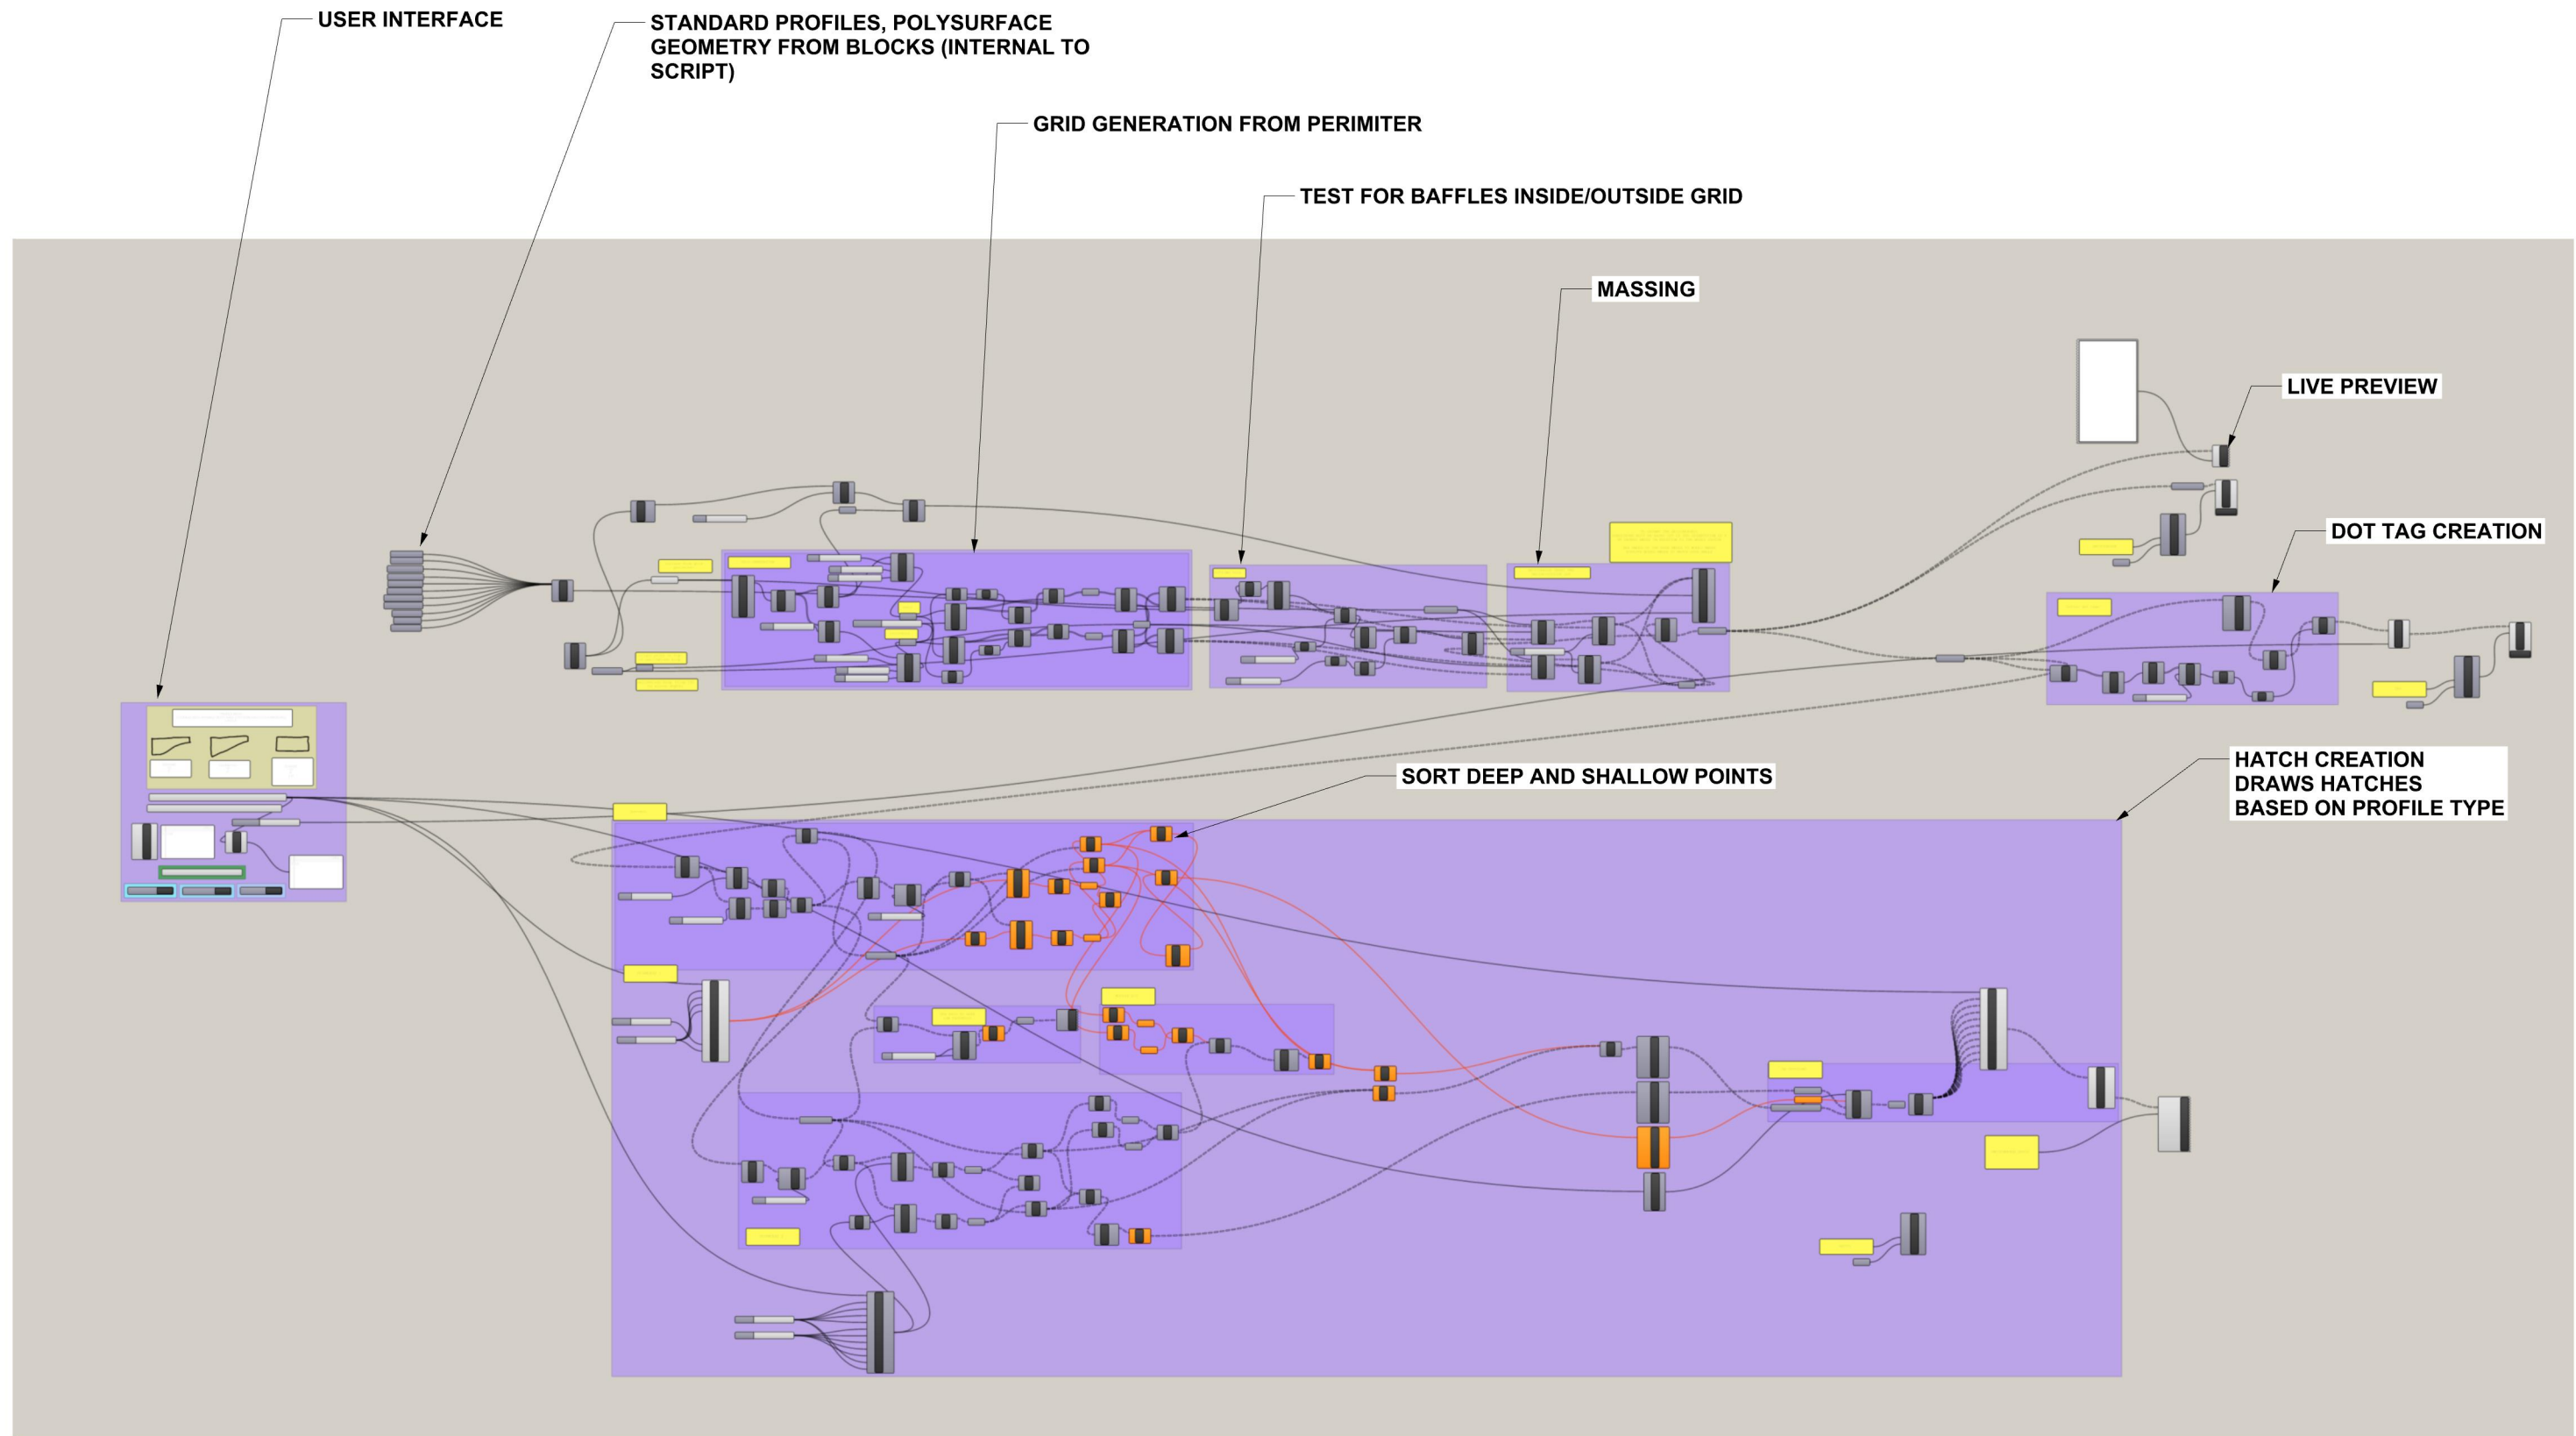

SWITCHBLADE, FLOW NOTATION


NTS 01

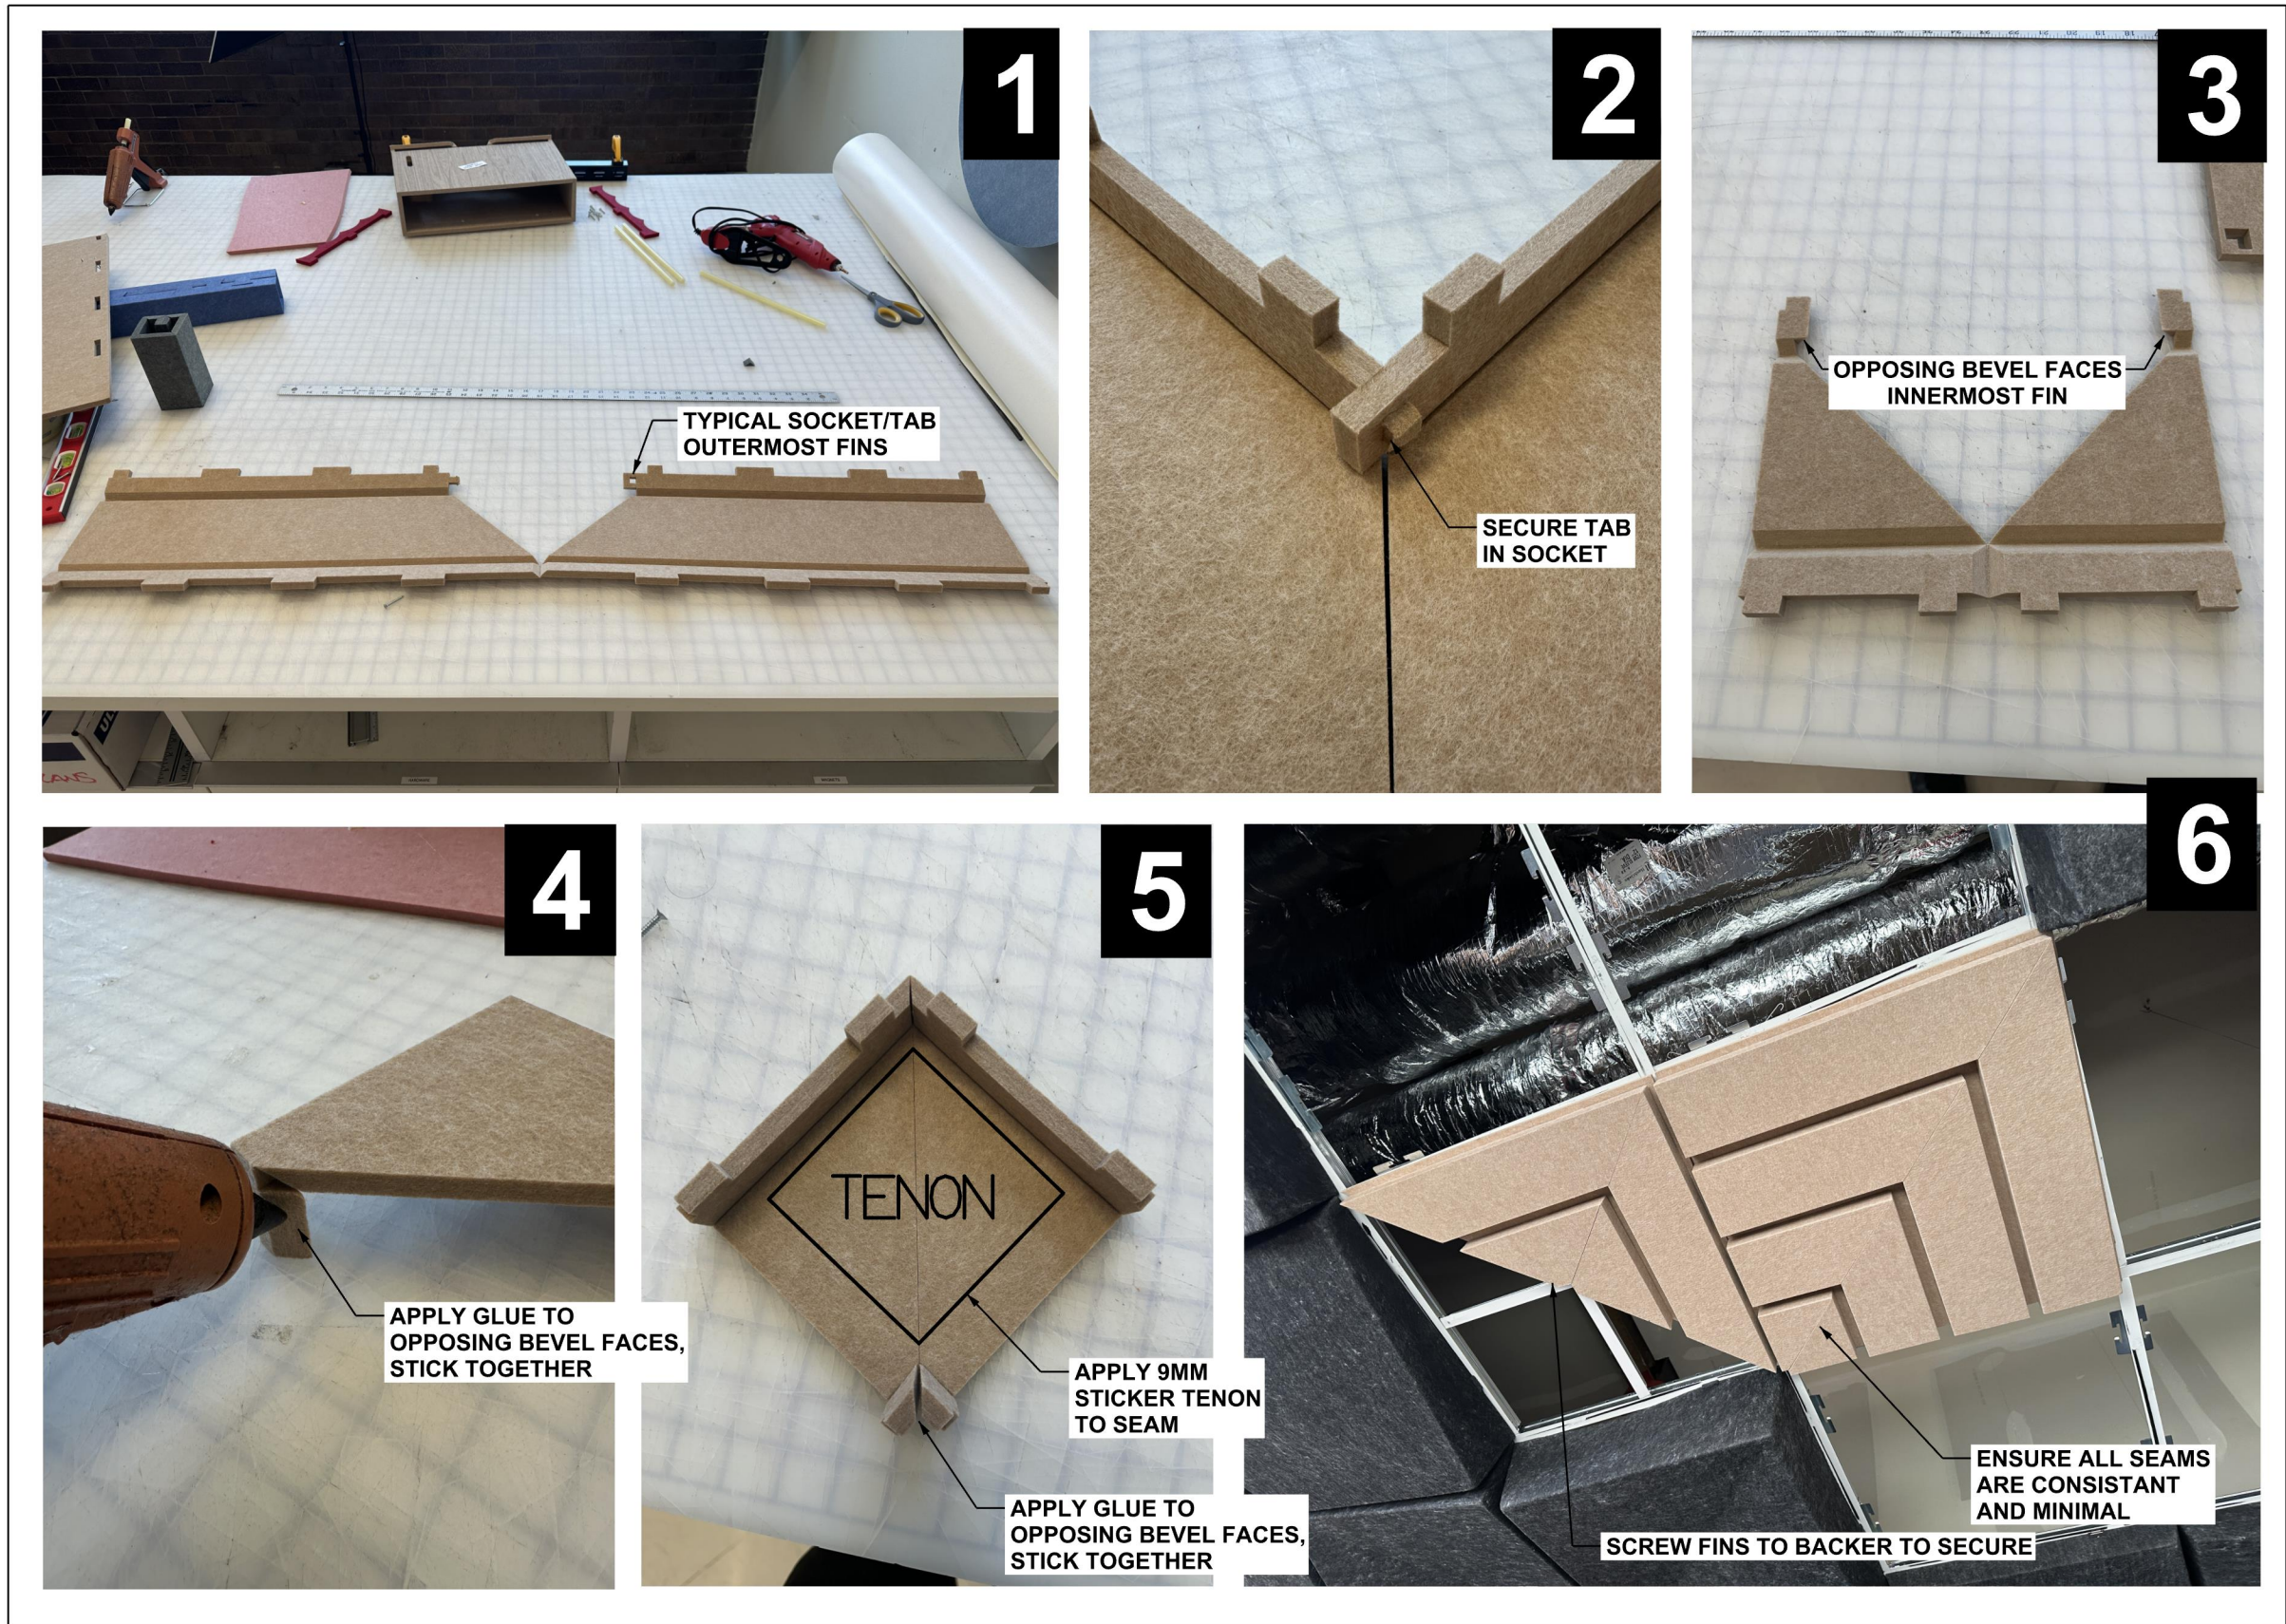

236542 BNY MELLON, LINEAR MITER DETAIL

01


NTS

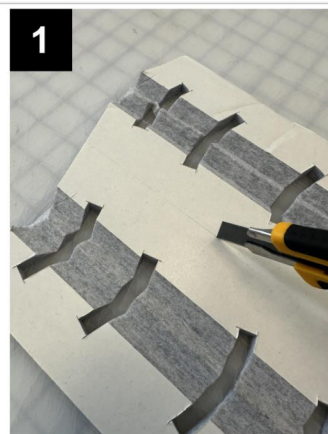


**LIGHTLY SCORE ALONG
CENTER OF ADHESIVE
FOR CLEAN TEAR-OUT**




TEAR AWAY ADHESIVE

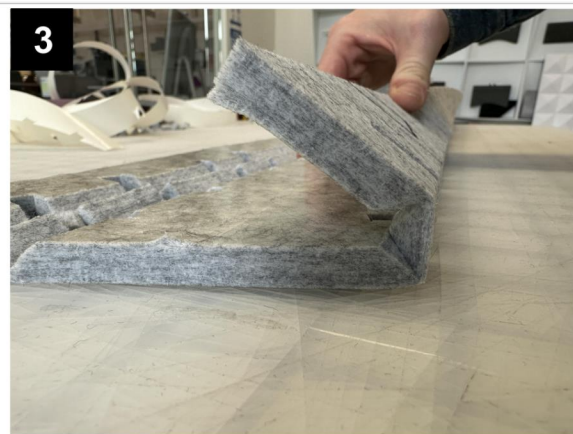

FOLD ALONG VCUTS

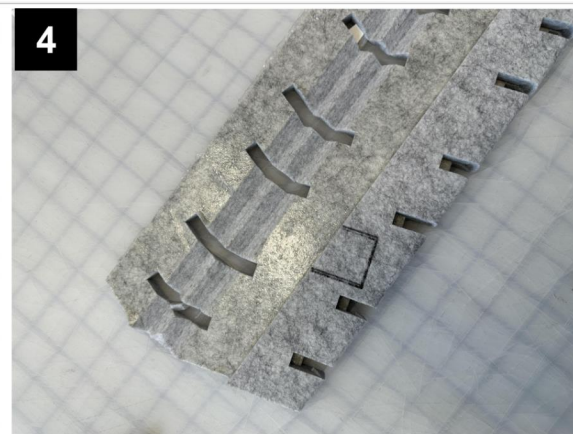


**Z CLIP OUTLINES ARE JOINED
WHEN FOLDS ARE COMPLETED**

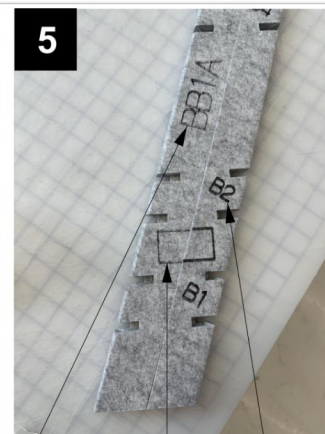



FELT RAIL TAG

BAFFLE TAG

Z CLIP OUTLINE

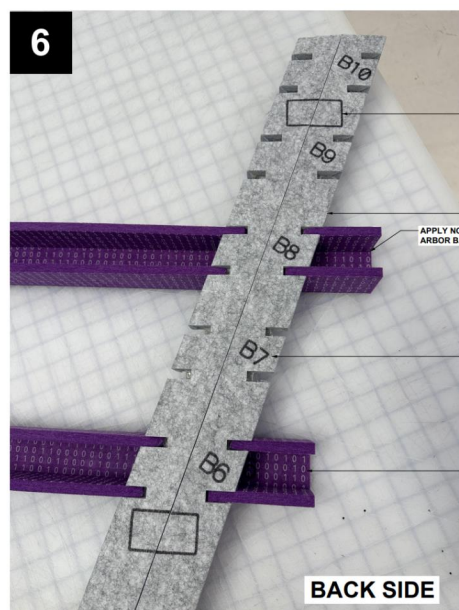


**BAFFLES FRICTION-FIT
INTO FELT RAIL NOTCHES
PLACE BAFFLES VIA MATCHING TAGS**

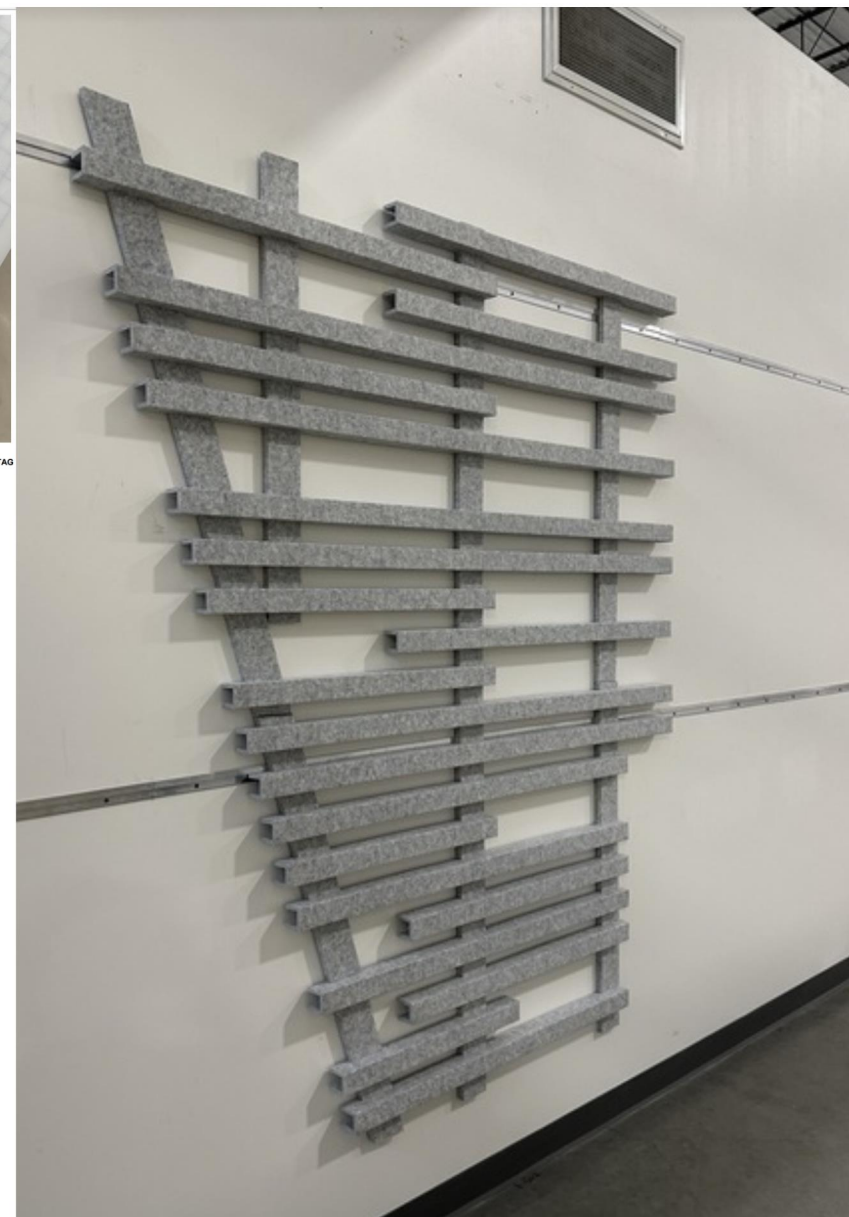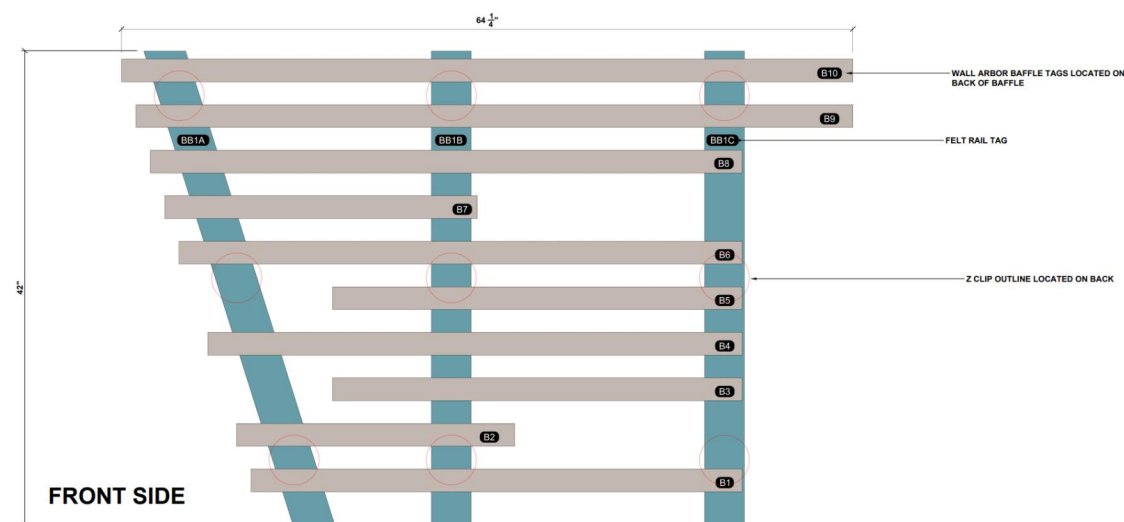

224409 WINK EYEWEAR, ANGLED FELT RAIL WALL ARBOR

NTS

(0

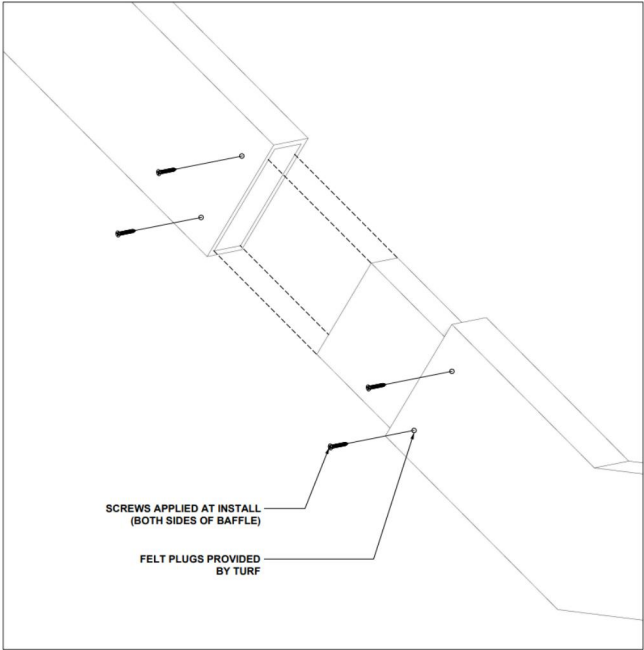


TENON DETAIL, FOLDED CUSTOM
NTS 03




214521, THE DOVE CHURCH, MITERED BEAM

NTS 01

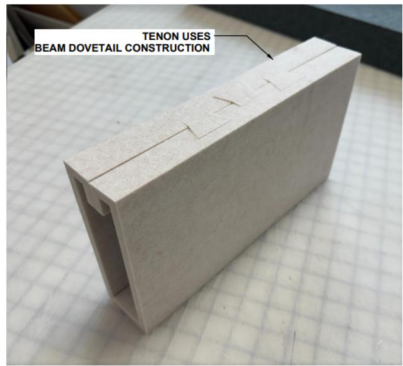

ASSEMBLED FOLDED TENON
NTS, FOR REPRESENTATION ONLY

05

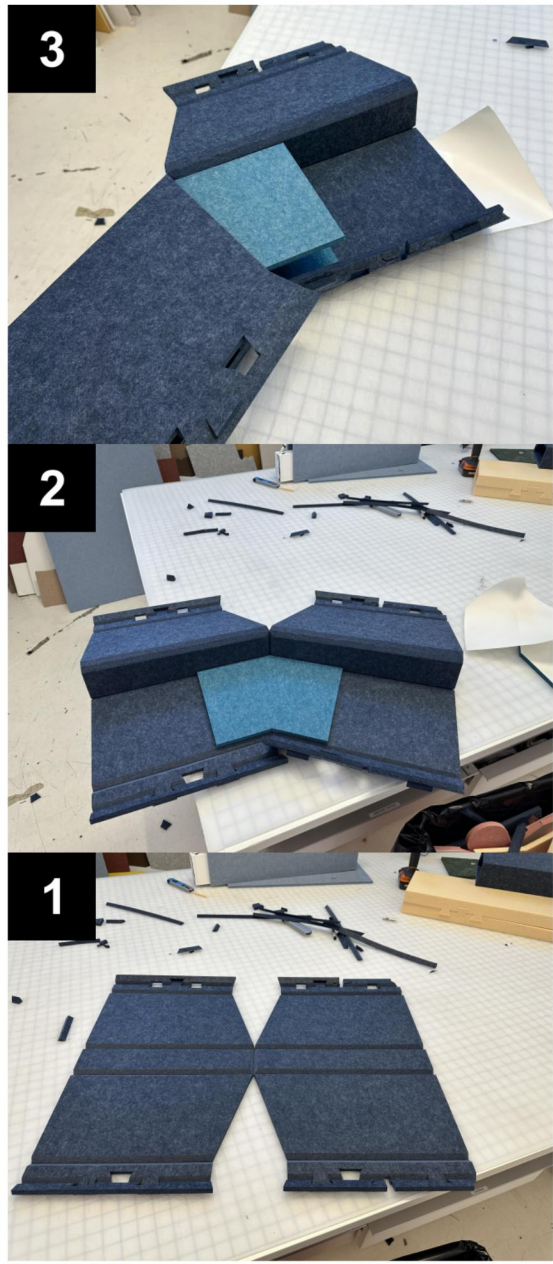


ASSEMBLY, "CT3"
NTS, FOR REPRESENTATION ONLY

04




ASSEMBLY, "CT1"
NTS, FOR REPRESENTATION ONLY

03

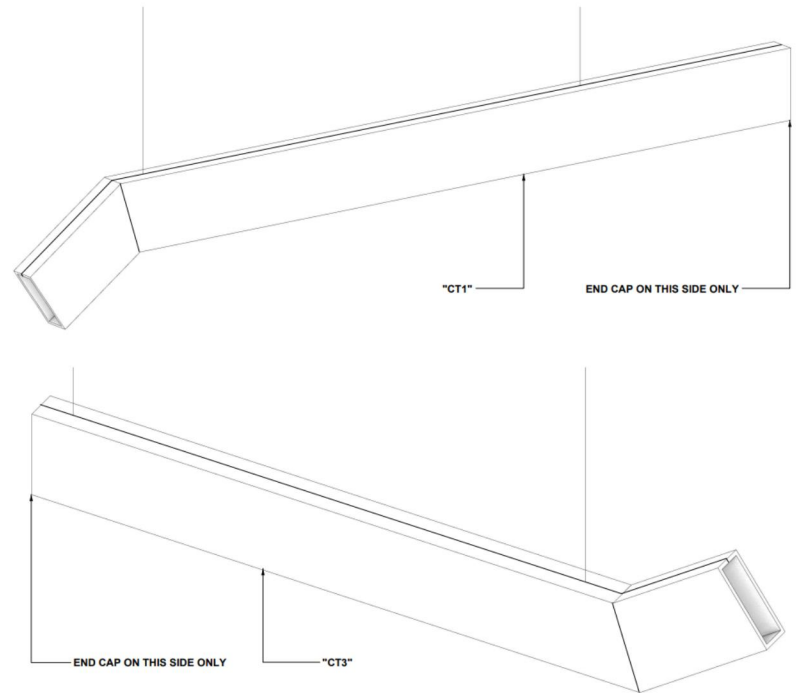

ASSEMBLED "CT1" & "CT3"
NTS, FOR REPRESENTATION ONLY

02

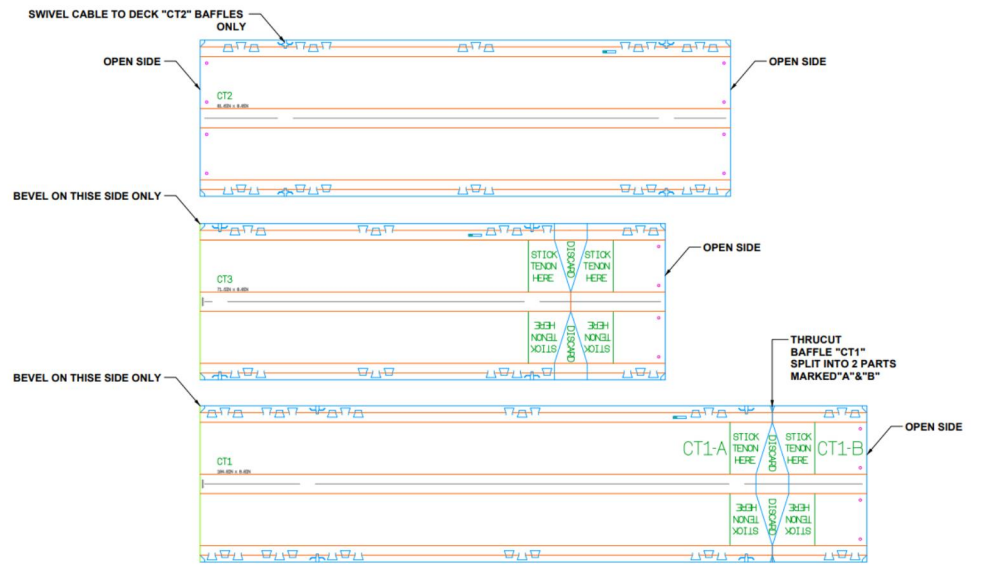

CUTFILES "CT1" - "CT3"
NTS, FOR REPRESENTATION ONLY

01




214521, THE DOVE CHURCH, MITERED BEAM ASSEMBLY

01

NTS


Step tile is a variation of barcode that works as typical, independant 24X24" tiles to make rising and falling patterns in a space. It sits between the new Arcade ceiling tile and the Labyrinth wall tile, acheiving another classical architectural look of descending and ascending soffits.

The design of step tile allows for a lot of customizability by a client without a complicated drawing set. The ability to use 3 typicals to make many different layouts gives it an edge over standard barcode for POF projects with complex patterns.

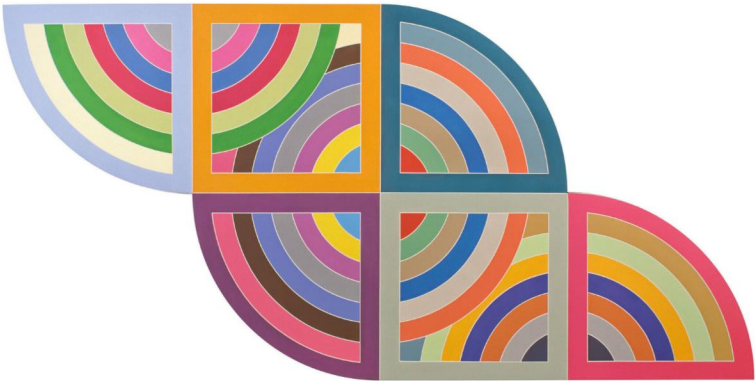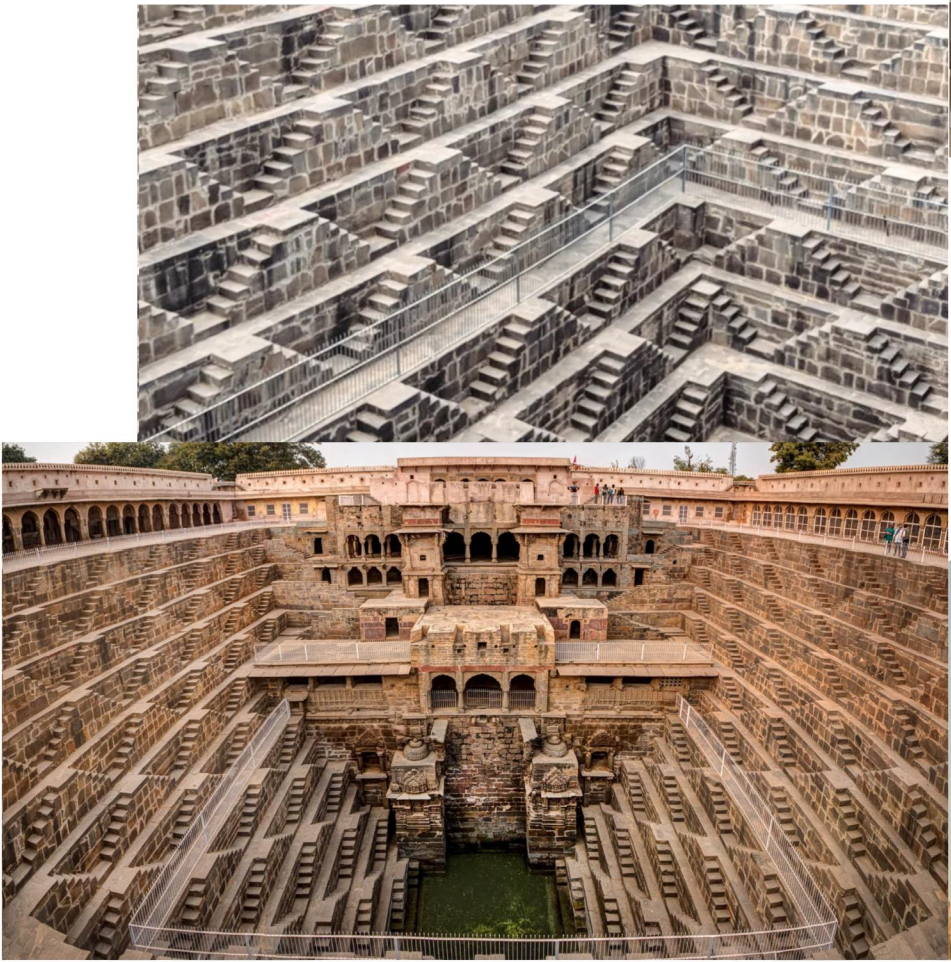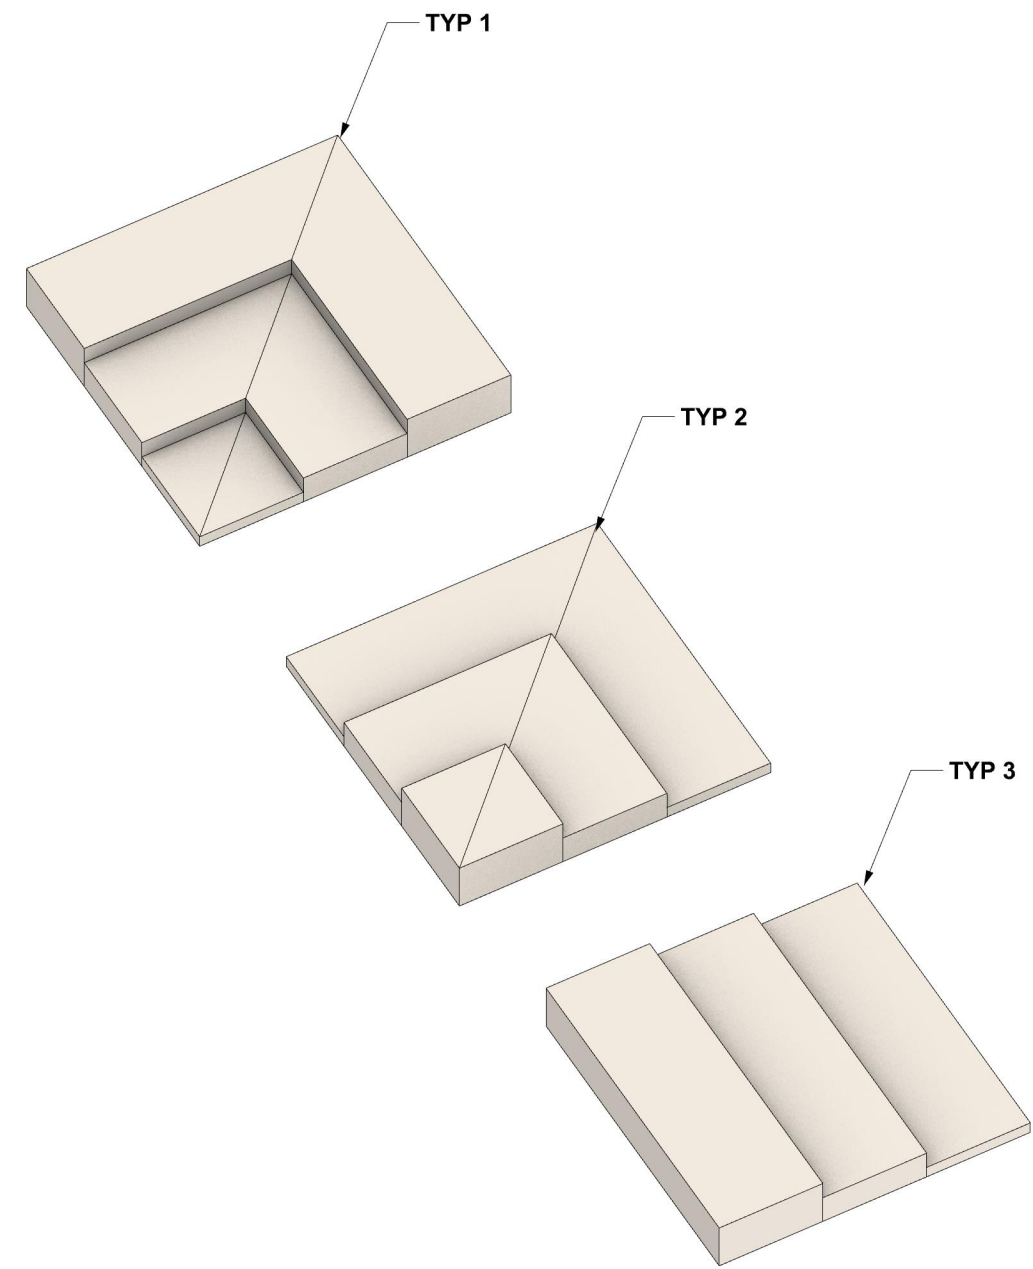



CONCEPT, STEP TILE

NTS 01

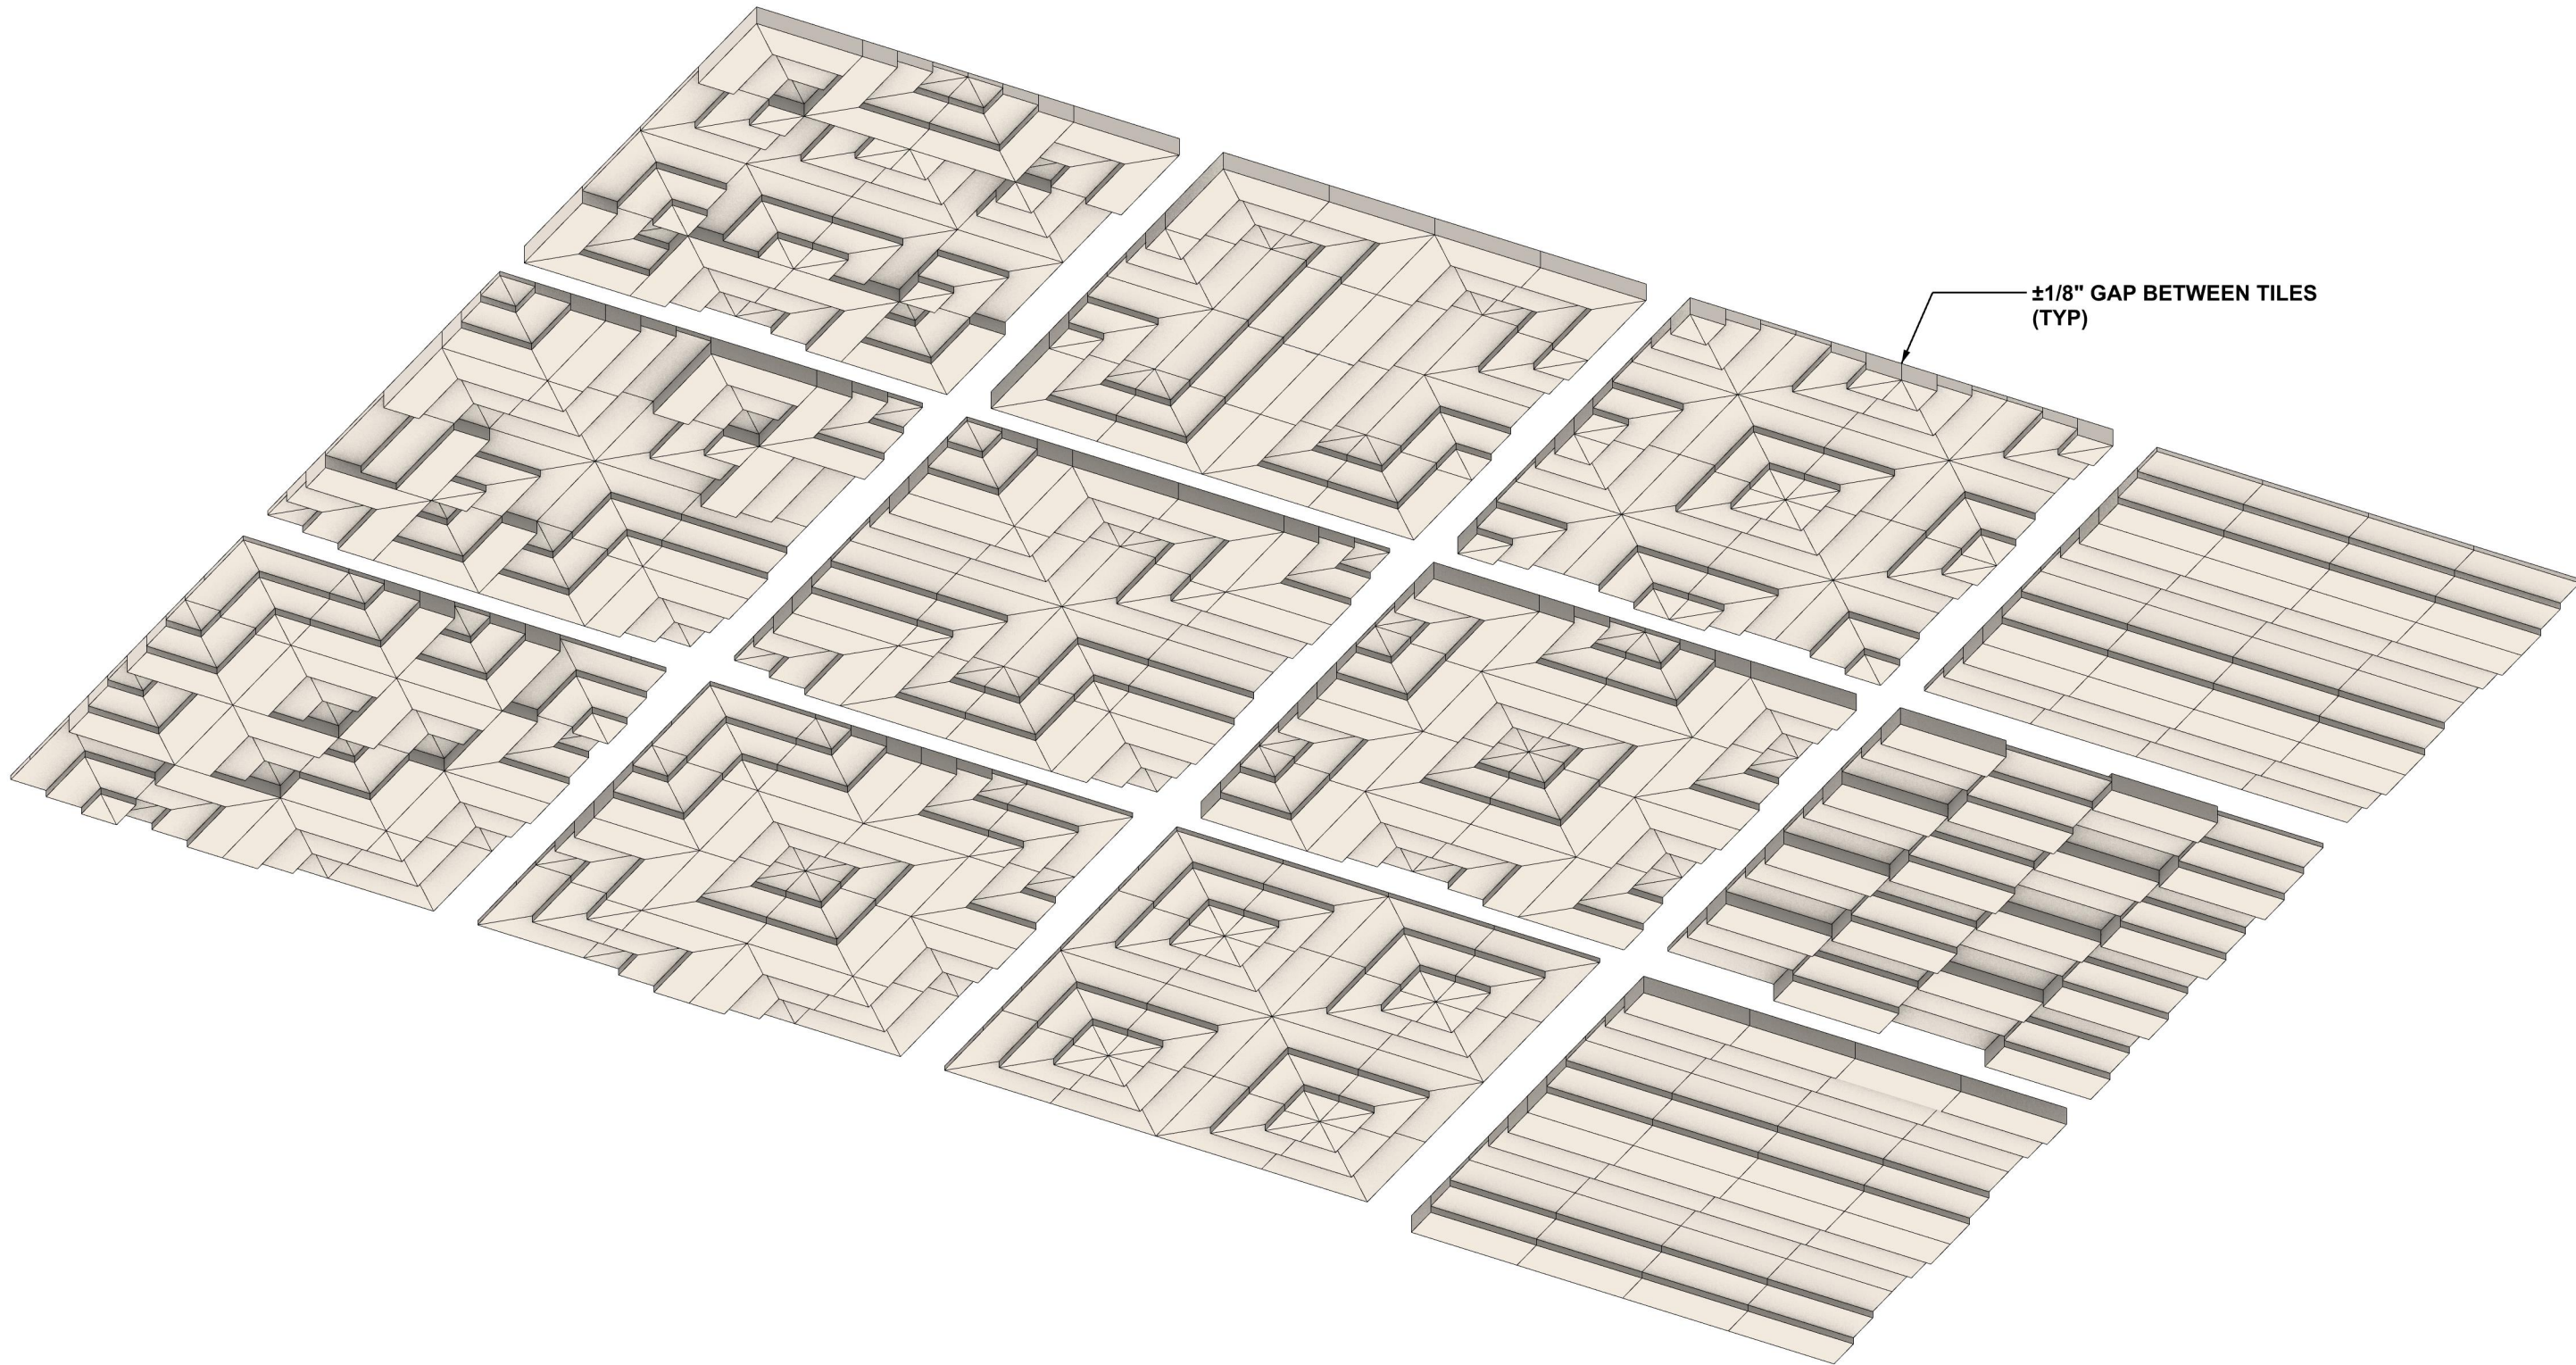


EXAMPLE LAYOUTS, STEP TILE

NTS 01

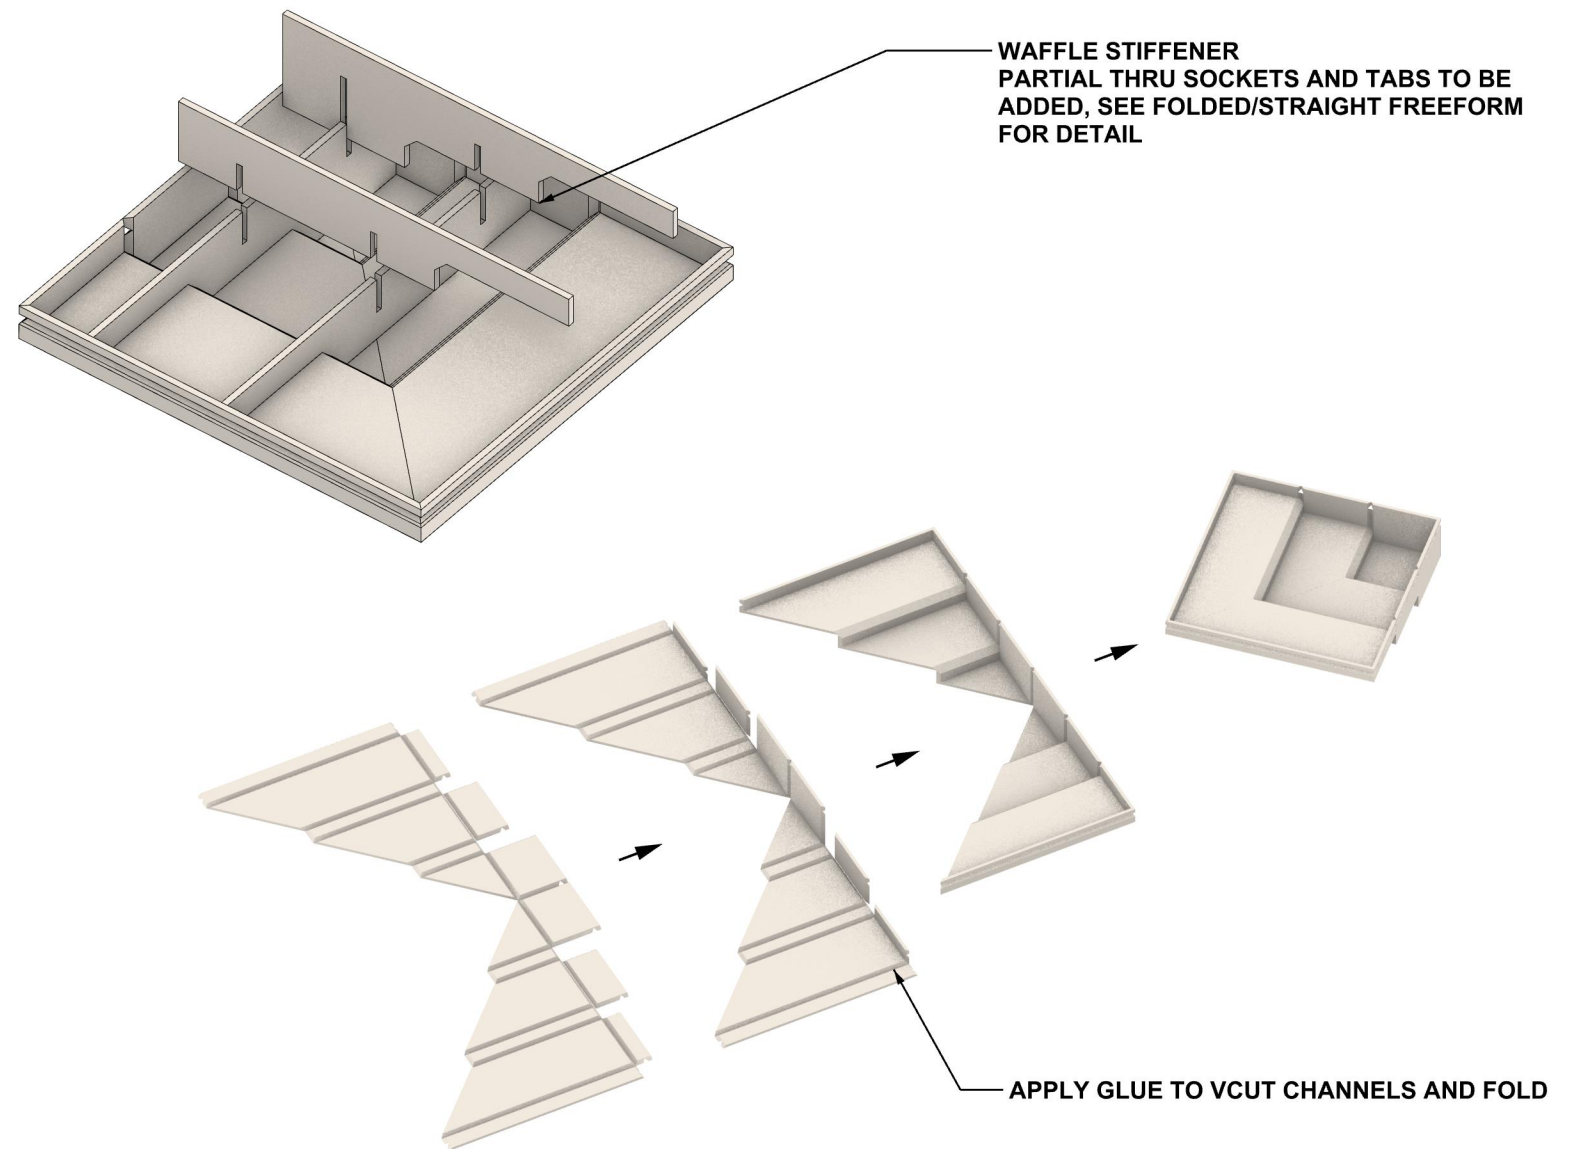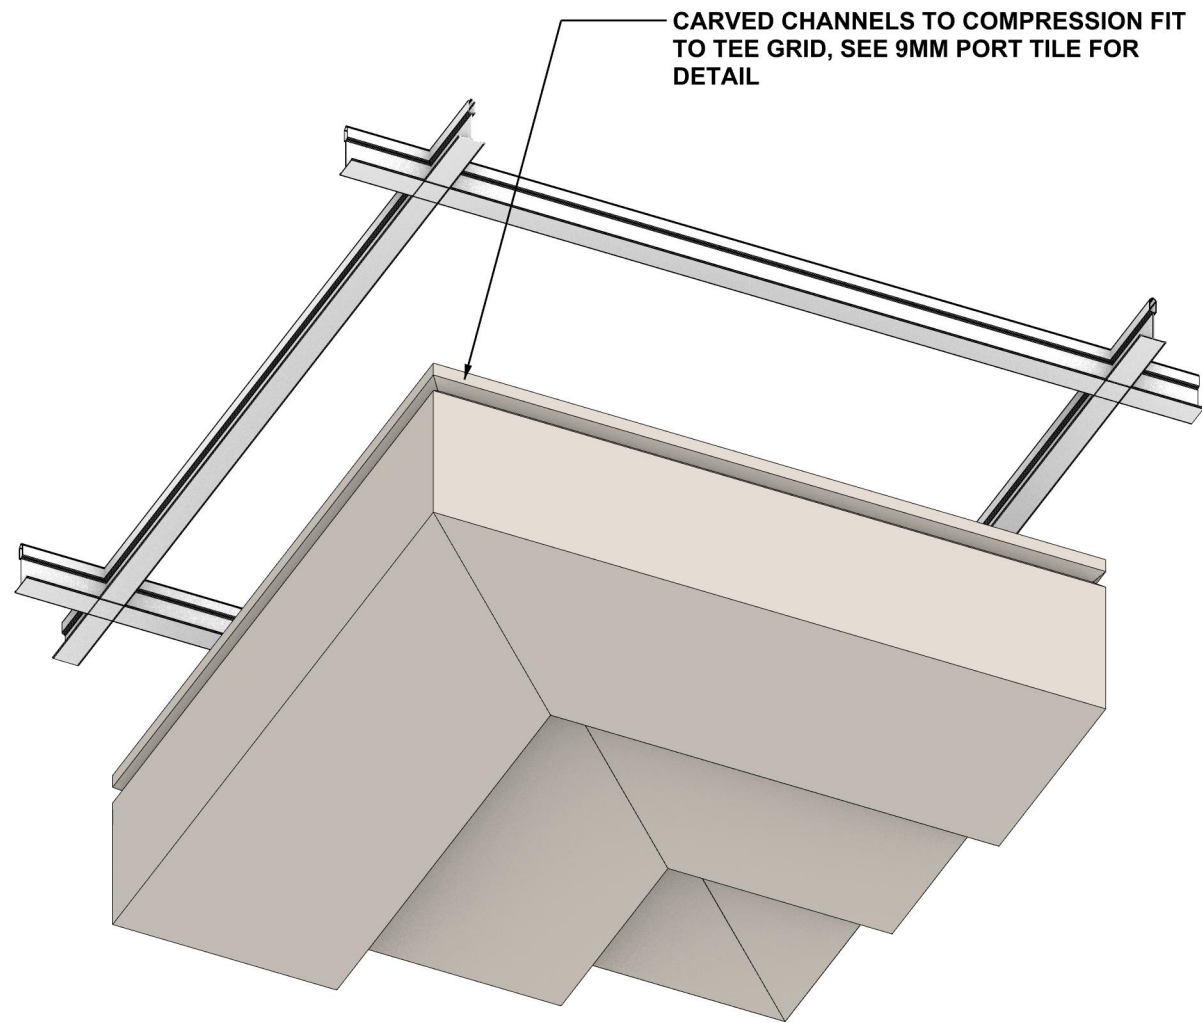

3 TILES PER SHEET
FLIP-OP REQUIRED
FOR TEE GRID
CHENNELS

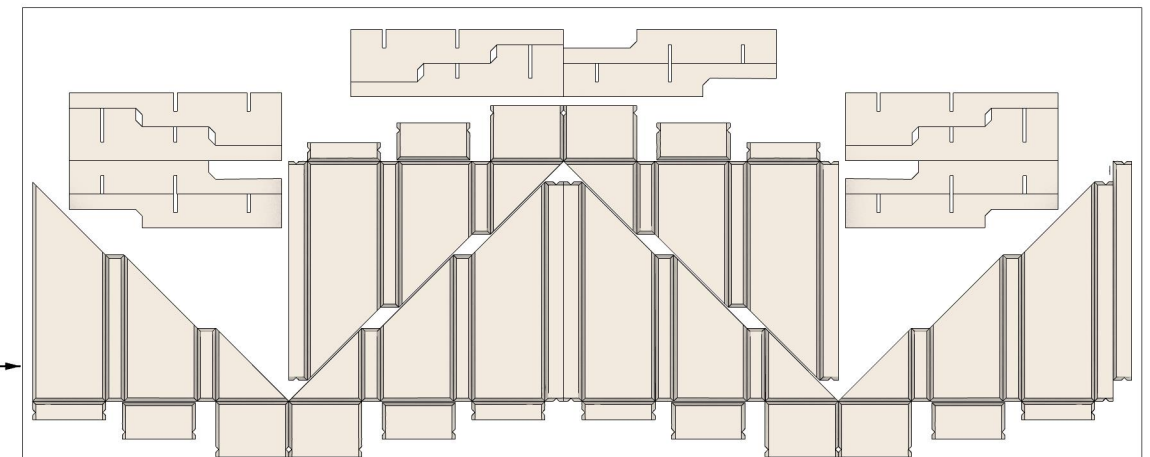

CONSTRUCTION, STEP TILE
NTS

01


Since the update to torrent tile I have completed several projects and trained the assembly team in the tagging system. I have also completed the details page for the products command, set to be released to design soon.

TORRENT WALL PANEL - PRODUCT DETAILS

SHOP SCHEDULES

TURF PANEL SCHEDULE						
PRODUCT	LOCATION	COLOR	CONNECTION	DIMENSIONS	SPACING	QTY.
TORRENT WALL PANEL A1	-	BASE: D00-TBD, PLEASE SPECIFY FINS: D00-TBD, PLEASE SPECIFY	Z-CLIP	30"W x 30"H x 6.5"D (NOMINAL DIMS)	N/A	#
TORRENT WALL PANEL A2	-	BASE: D00-TBD, PLEASE SPECIFY FINS: D00-TBD, PLEASE SPECIFY	Z-CLIP	30"W x 30"H x 6.5"D (NOMINAL DIMS)	N/A	#
TORRENT WALL PANEL B1	-	BASE: D00-TBD, PLEASE SPECIFY FINS: D00-TBD, PLEASE SPECIFY	Z-CLIP	30"W x 30"H x 6.5"D (NOMINAL DIMS)	N/A	#
TORRENT WALL PANEL B2	-	BASE: D00-TBD, PLEASE SPECIFY FINS: D00-TBD, PLEASE SPECIFY	Z-CLIP	30"W x 30"H x 6.5"D (NOMINAL DIMS)	N/A	#
TORRENT WALL PANEL B3	-	BASE: D00-TBD, PLEASE SPECIFY FINS: D00-TBD, PLEASE SPECIFY	Z-CLIP	30"W x 30"H x 6.5"D (NOMINAL DIMS)	N/A	#
TORRENT WALL PANEL B4	-	BASE: D00-TBD, PLEASE SPECIFY FINS: D00-TBD, PLEASE SPECIFY	Z-CLIP	30"W x 30"H x 6.5"D (NOMINAL DIMS)	N/A	#
TORRENT WALL PANEL C	-	BASE: D00-TBD, PLEASE SPECIFY FINS: D00-TBD, PLEASE SPECIFY	Z-CLIP	30"W x 30"H x 2.5"D (NOMINAL DIMS)	N/A	#

PRODUCT DETAILS

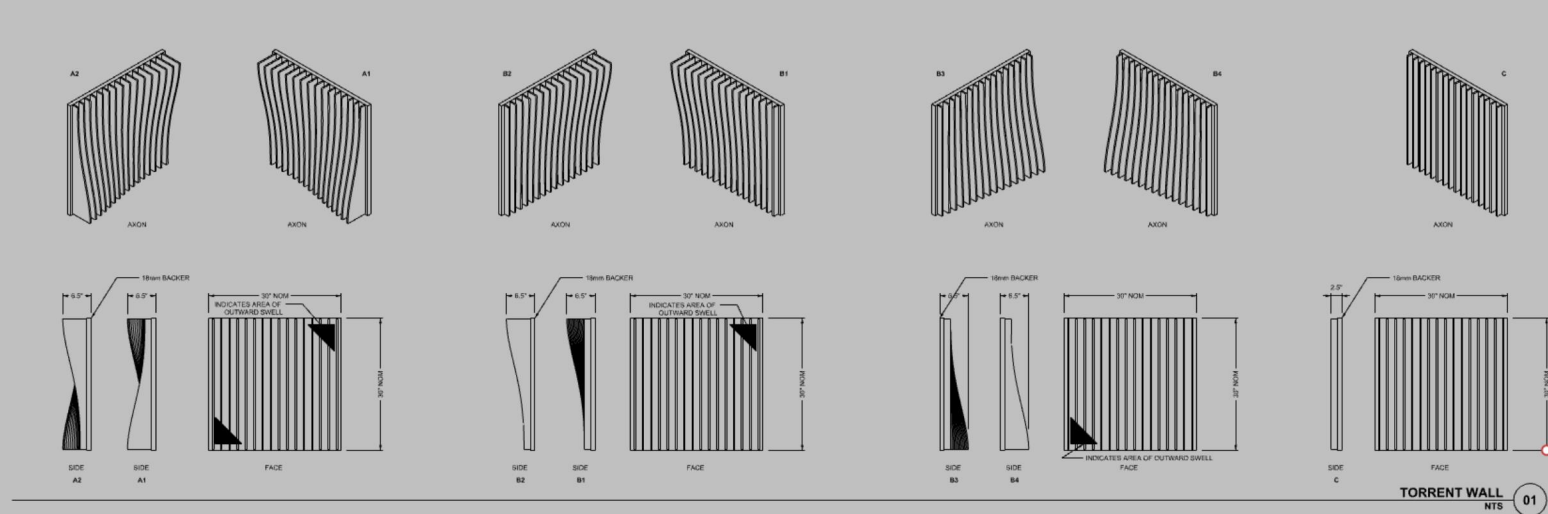

PRODUCTION SCHEDULES

TURF PANEL SCHEDULE							CNC	3D
PRODUCT	TAG	LOCATION	COLOR	CONN.	DIM. (L x W x D)	QTY.	✓	✓
TORRENT WALL PANEL A1	--	--	BASE: 04 LIGHT GREY FINS: 05 WHITE	Z CLIP	30"L x 30"W x 6.5"D	--		
TORRENT WALL PANEL A2	--	--	BASE: 04 LIGHT GREY FINS: 05 WHITE	Z CLIP	30"L x 30"W x 6.5"D	--		
TORRENT WALL PANEL B1	--	--	BASE: 04 LIGHT GREY FINS: 05 WHITE	Z CLIP	30"L x 30"W x 6.5"D	--		
TORRENT WALL PANEL B2	--	--	BASE: 04 LIGHT GREY FINS: 05 WHITE	Z CLIP	30"L x 30"W x 6.5"D	--		
TORRENT WALL PANEL B3	--	--	BASE: 04 LIGHT GREY FINS: 05 WHITE	Z CLIP	30"L x 30"W x 6.5"D	--		
TORRENT WALL PANEL B4	--	--	BASE: 04 LIGHT GREY FINS: 05 WHITE	Z CLIP	30"L x 30"W x 6.5"D	--		
TORRENT WALL PANEL C	--	--	BASE: 04 LIGHT GREY FINS: 05 WHITE	Z CLIP	30"L x 30"W x 2.5"D	--		

REFERENCE
HARDWARE
COMMAND

USE HARDWARE COMMAND TO CALL
SHOPS AND PRODUCTION SCHEDULES


TOTAL PANEL COUNT --

PRODUCT NOTES

Standard Torrent Wall panel sizes are 30"H x 30"W x 6.5"D. Anything outside the bounds of this ruleset will require custom efforts.

RELATED PARAMETRIC COMMANDS

3D / 2D Blocks can be called via the "Products" command, but currently require manual layout design.

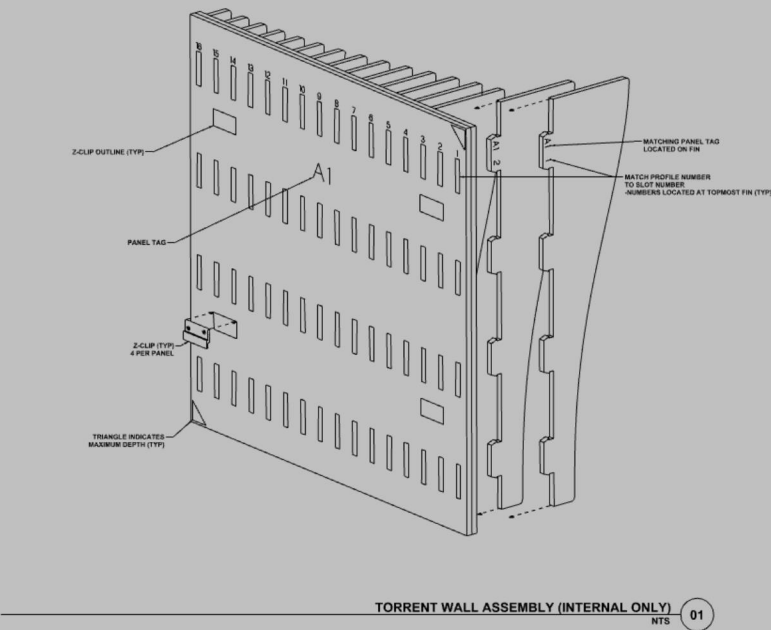

9MM FILL PANEL - PRODUCT DETAILS

SHOP SCHEDULES

TURF PANEL SCHEDULE						
PRODUCT	LOCATION	COLOR	CONNECTION	DIMENSIONS	SQFT	QTY.
9MM FILL PANEL FL1	-	TBD, PLEASE SPECIFY	ADHESIVE BY OTHERS	48"L x 1"W x 9MM MATERIAL	#SQFT	#
9MM FILL PANEL FL3	-	TBD, PLEASE SPECIFY	ADHESIVE BY OTHERS	48"L x 3"W x 9MM MATERIAL	#SQFT	#
9MM FILL PANEL FL6	-	TBD, PLEASE SPECIFY	ADHESIVE BY OTHERS	48"L x 6"W x 9MM MATERIAL	#SQFT	#


PRODUCTION SCHEDULES

TURF PANEL SCHEDULE									
PRODUCT	TAG	LOCATION	COLOR	CONN.	DIM. (L x W x D)	QTY.	✓	✓	✓
9MM FILL PANEL FL1	FL1	-	TBD, PLEASE SPECIFY	NON ADHESIVE / BY OTHERS	48"L x 1"W x 9MM	-			
9MM FILL PANEL FL3	FL3	-	TBD, PLEASE SPECIFY	NON ADHESIVE / BY OTHERS	48"L x 3"W x 9MM	-			
9MM FILL PANEL FL6	FL6	-	TBD, PLEASE SPECIFY	NON ADHESIVE / BY OTHERS	48"L x 6"W x 9MM	-			
TOTAL PANEL COUNT						-			


REFERENCE
HARDWARE
COMMAND

USE HARDWARE COMMAND TO CALL
SHOPS AND PRODUCTION SCHEDULES

PANEL TYPES

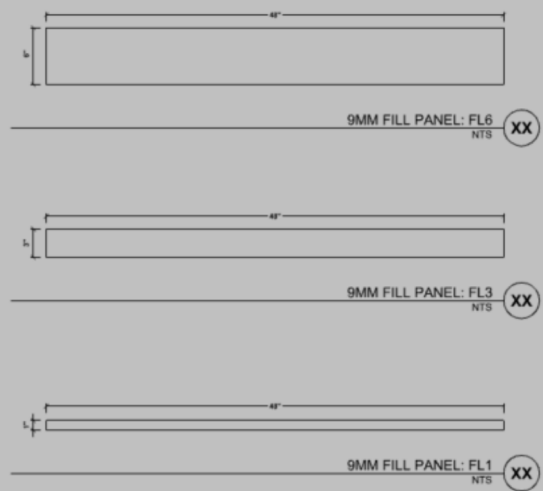


TRIM PROVIDED SHEET MATERIAL TO OUTLET DIMENSIONS
AND PRODUCT DEPTH, CUT FLAT OR BEVEL AT A 45° ANGLE

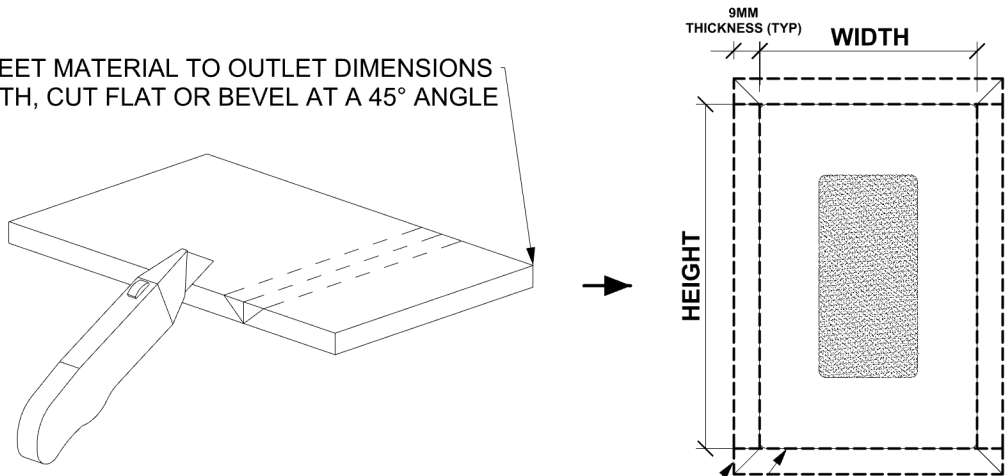

FOR FLAT EDGES:
TOP/BOTTOM PANELS ARE 18MM LONGER THAN OUTLET WIDTH

FOR BEVELED EDGES:
CUT ALONG INTERIOR DIMENSIONS

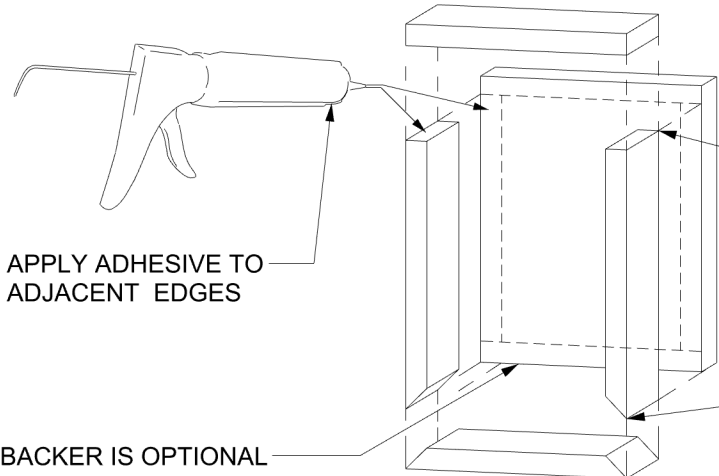

FLAT CUT

BEVEL CUT

TURF PRODUCT
REFER TO PRODUCT DETAILS
FOR TRIMMING INSTRUCTIONS


9MM FILL PANEL TRIM GUIDE

NTS 01


To give our panel products the same capability as our 9mm baffle options, I have started development on a contour panel script for walls and ceilings. One grasshopper script is used to obtain outputs for all three types.

The new product can be customized exactly like our 9mm ceilings, and has the potential to output wall mounted straight baffle, ridge baffle, and contour baffle.


Built off of the torrent wall construction, the tabbed 18mm method has been proven in field.

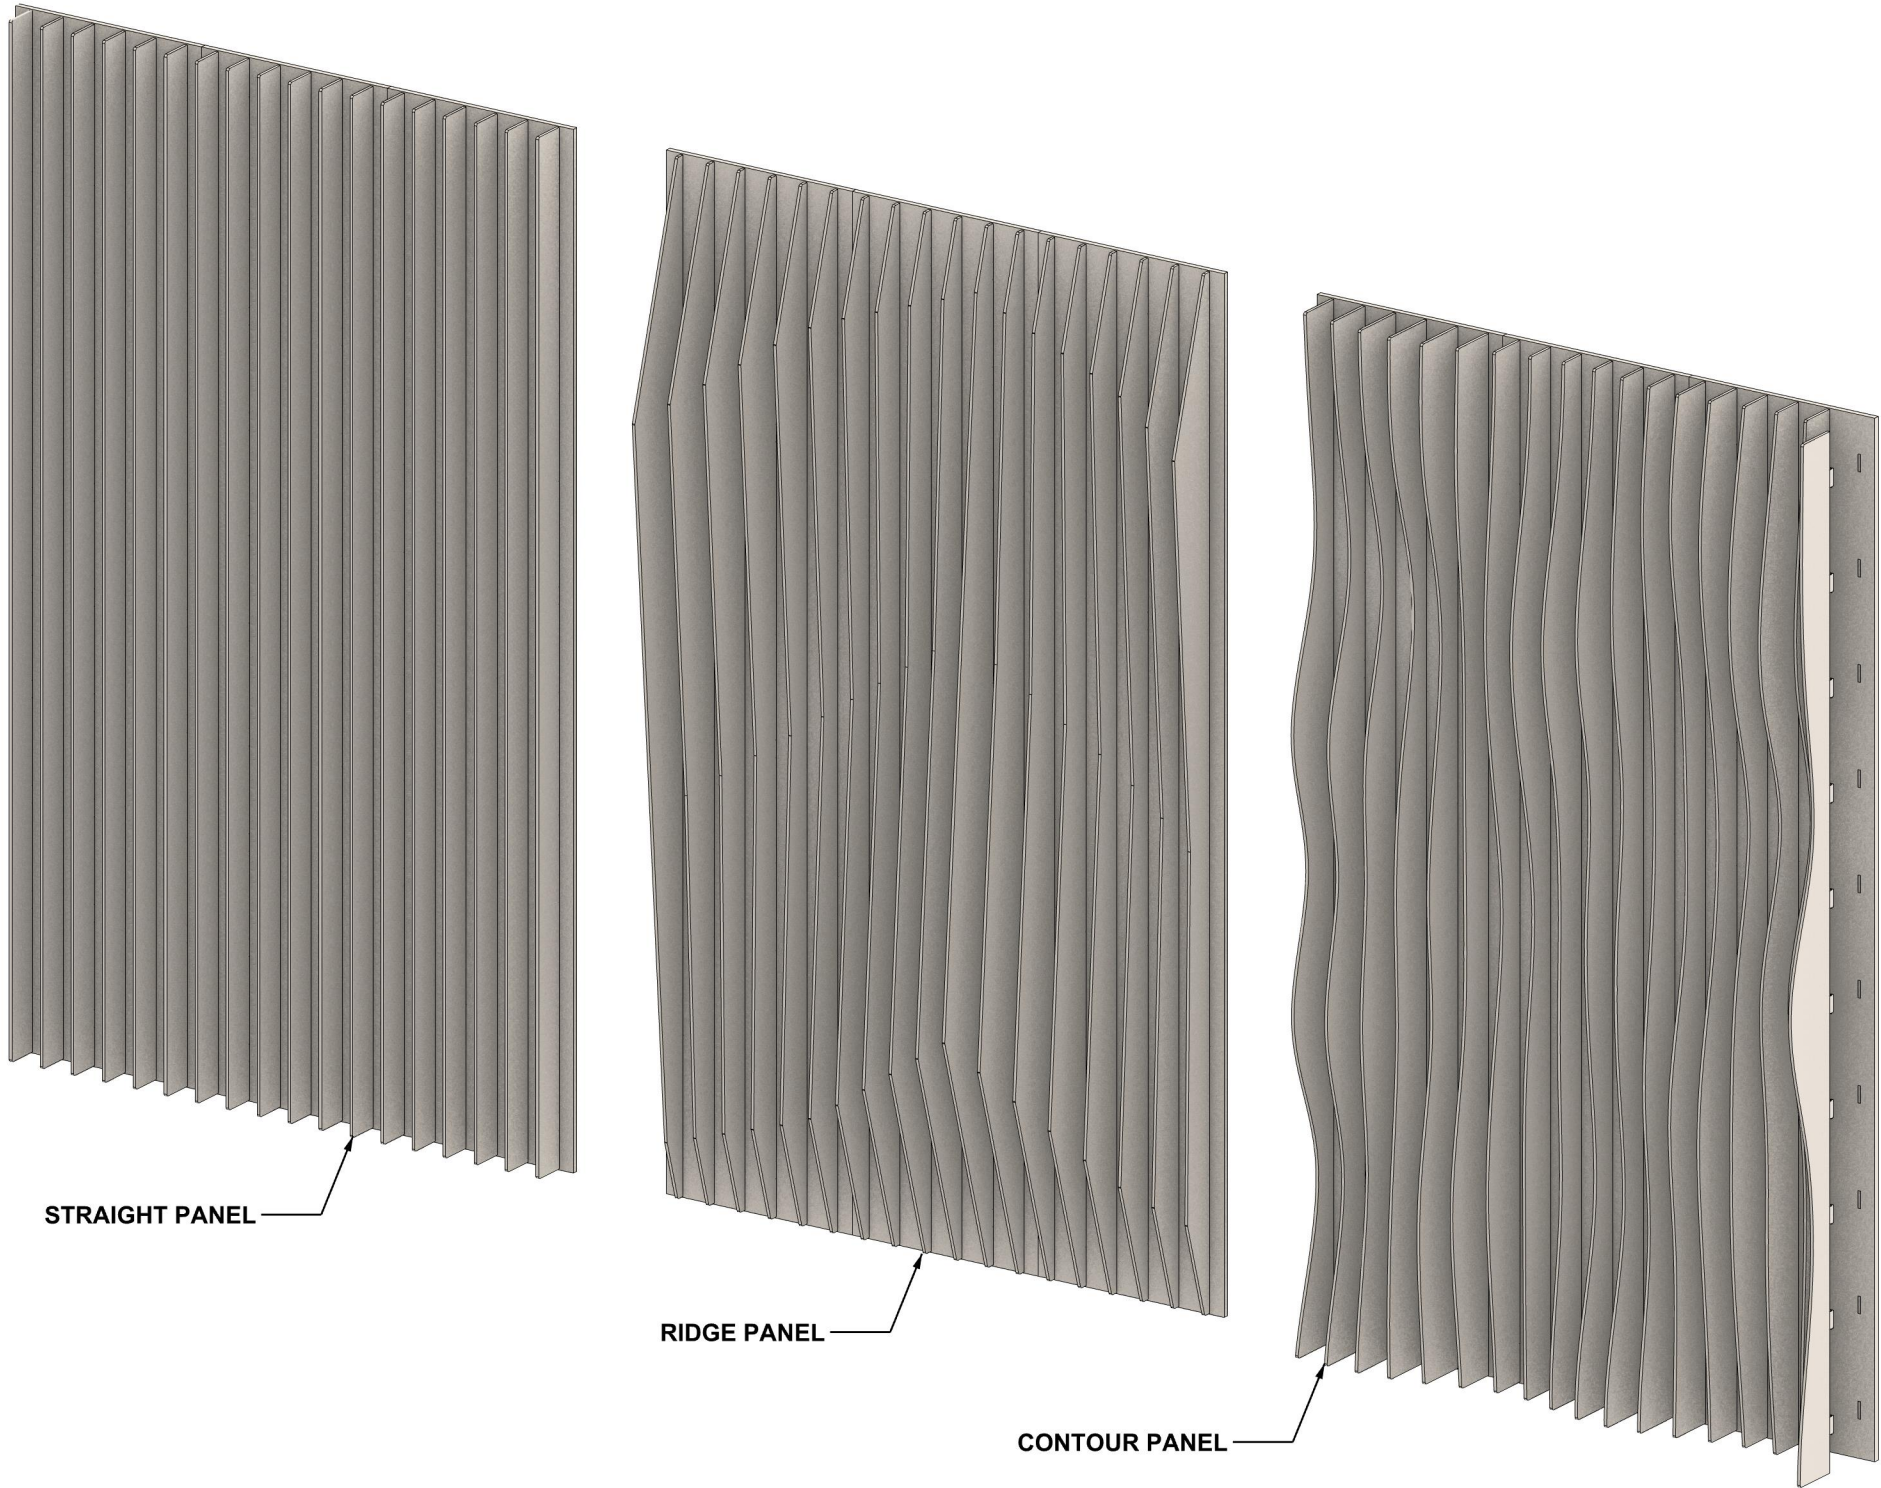


PRODUCT DEVELOPMENT - 9MM BAFFLE WALL (MASSING FROM SCRIPT OUTPUT)
NTS

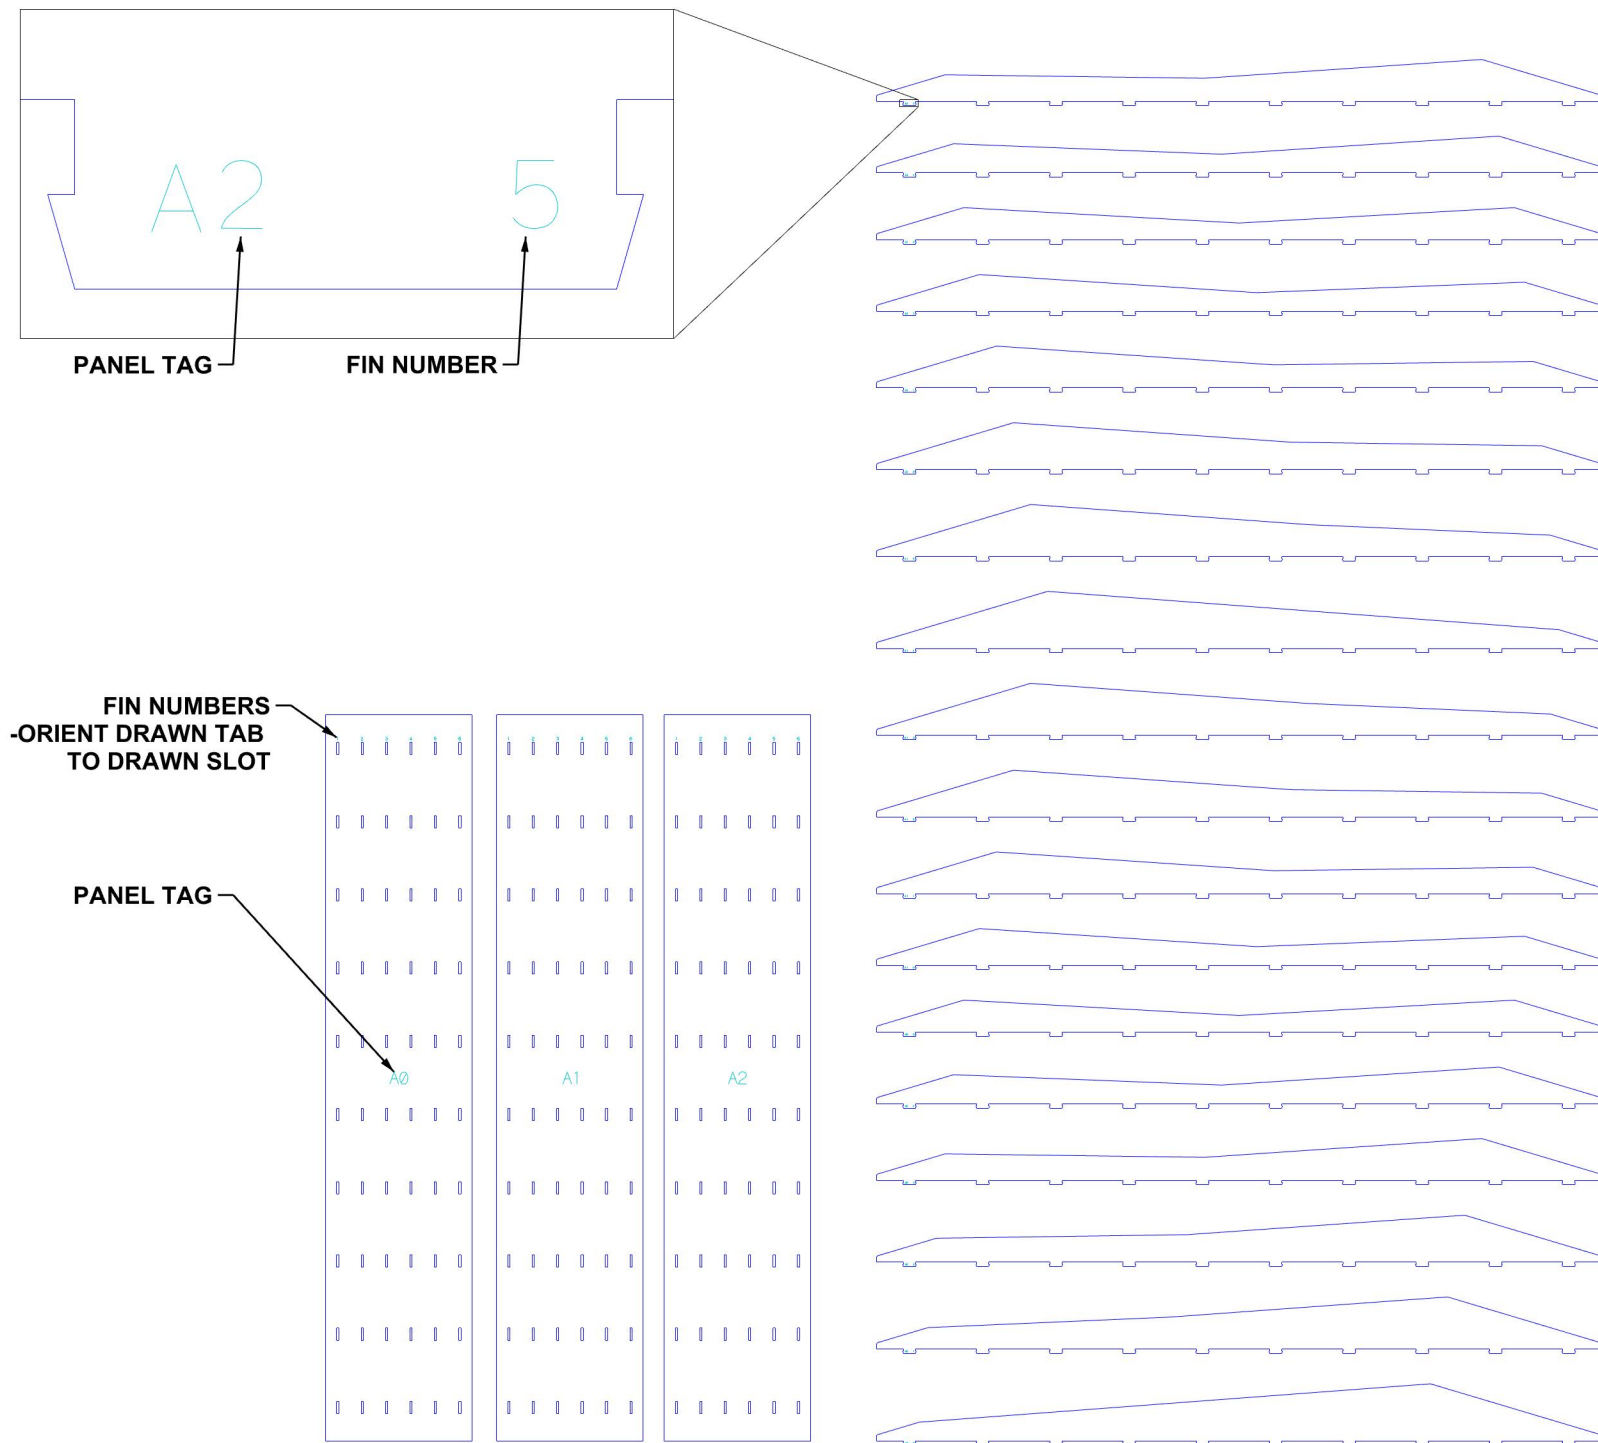

CONTOUR WALL OUTPUTS (CUTFILES)
NTS 01

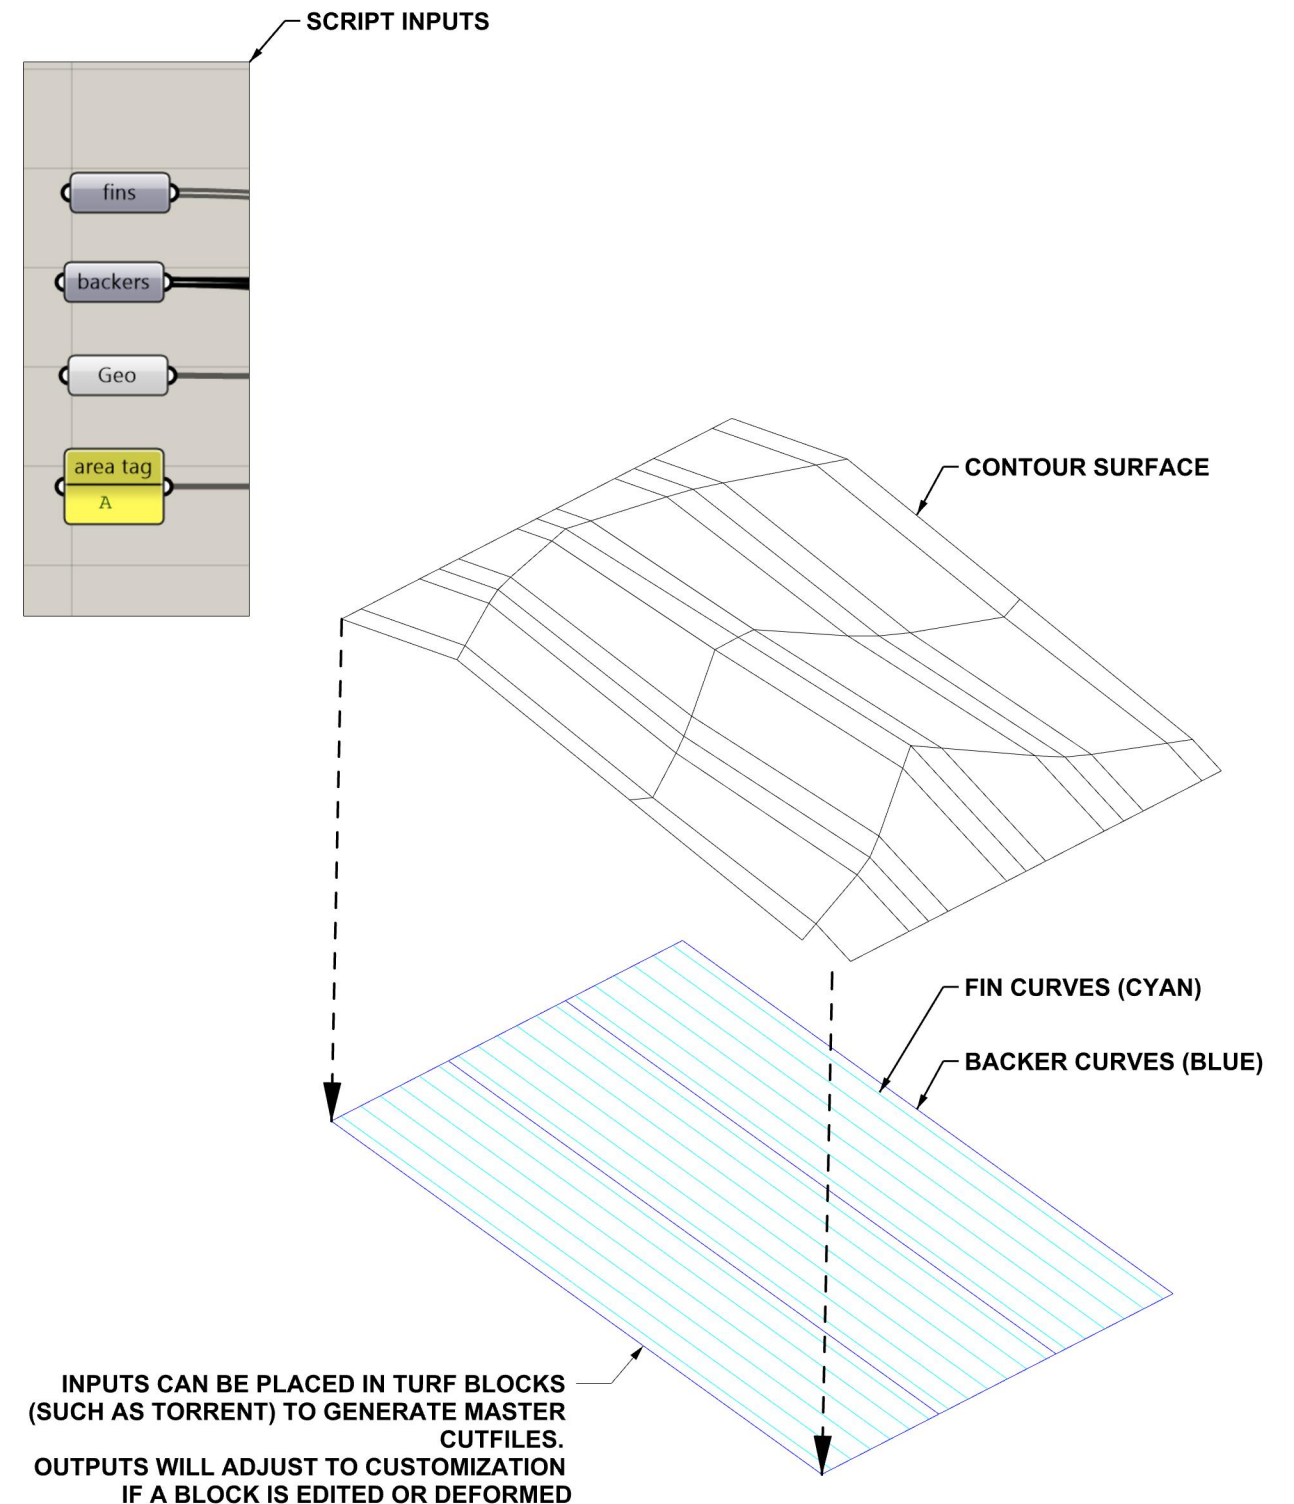


CONTOUR WALL INPUTS
NTS 01

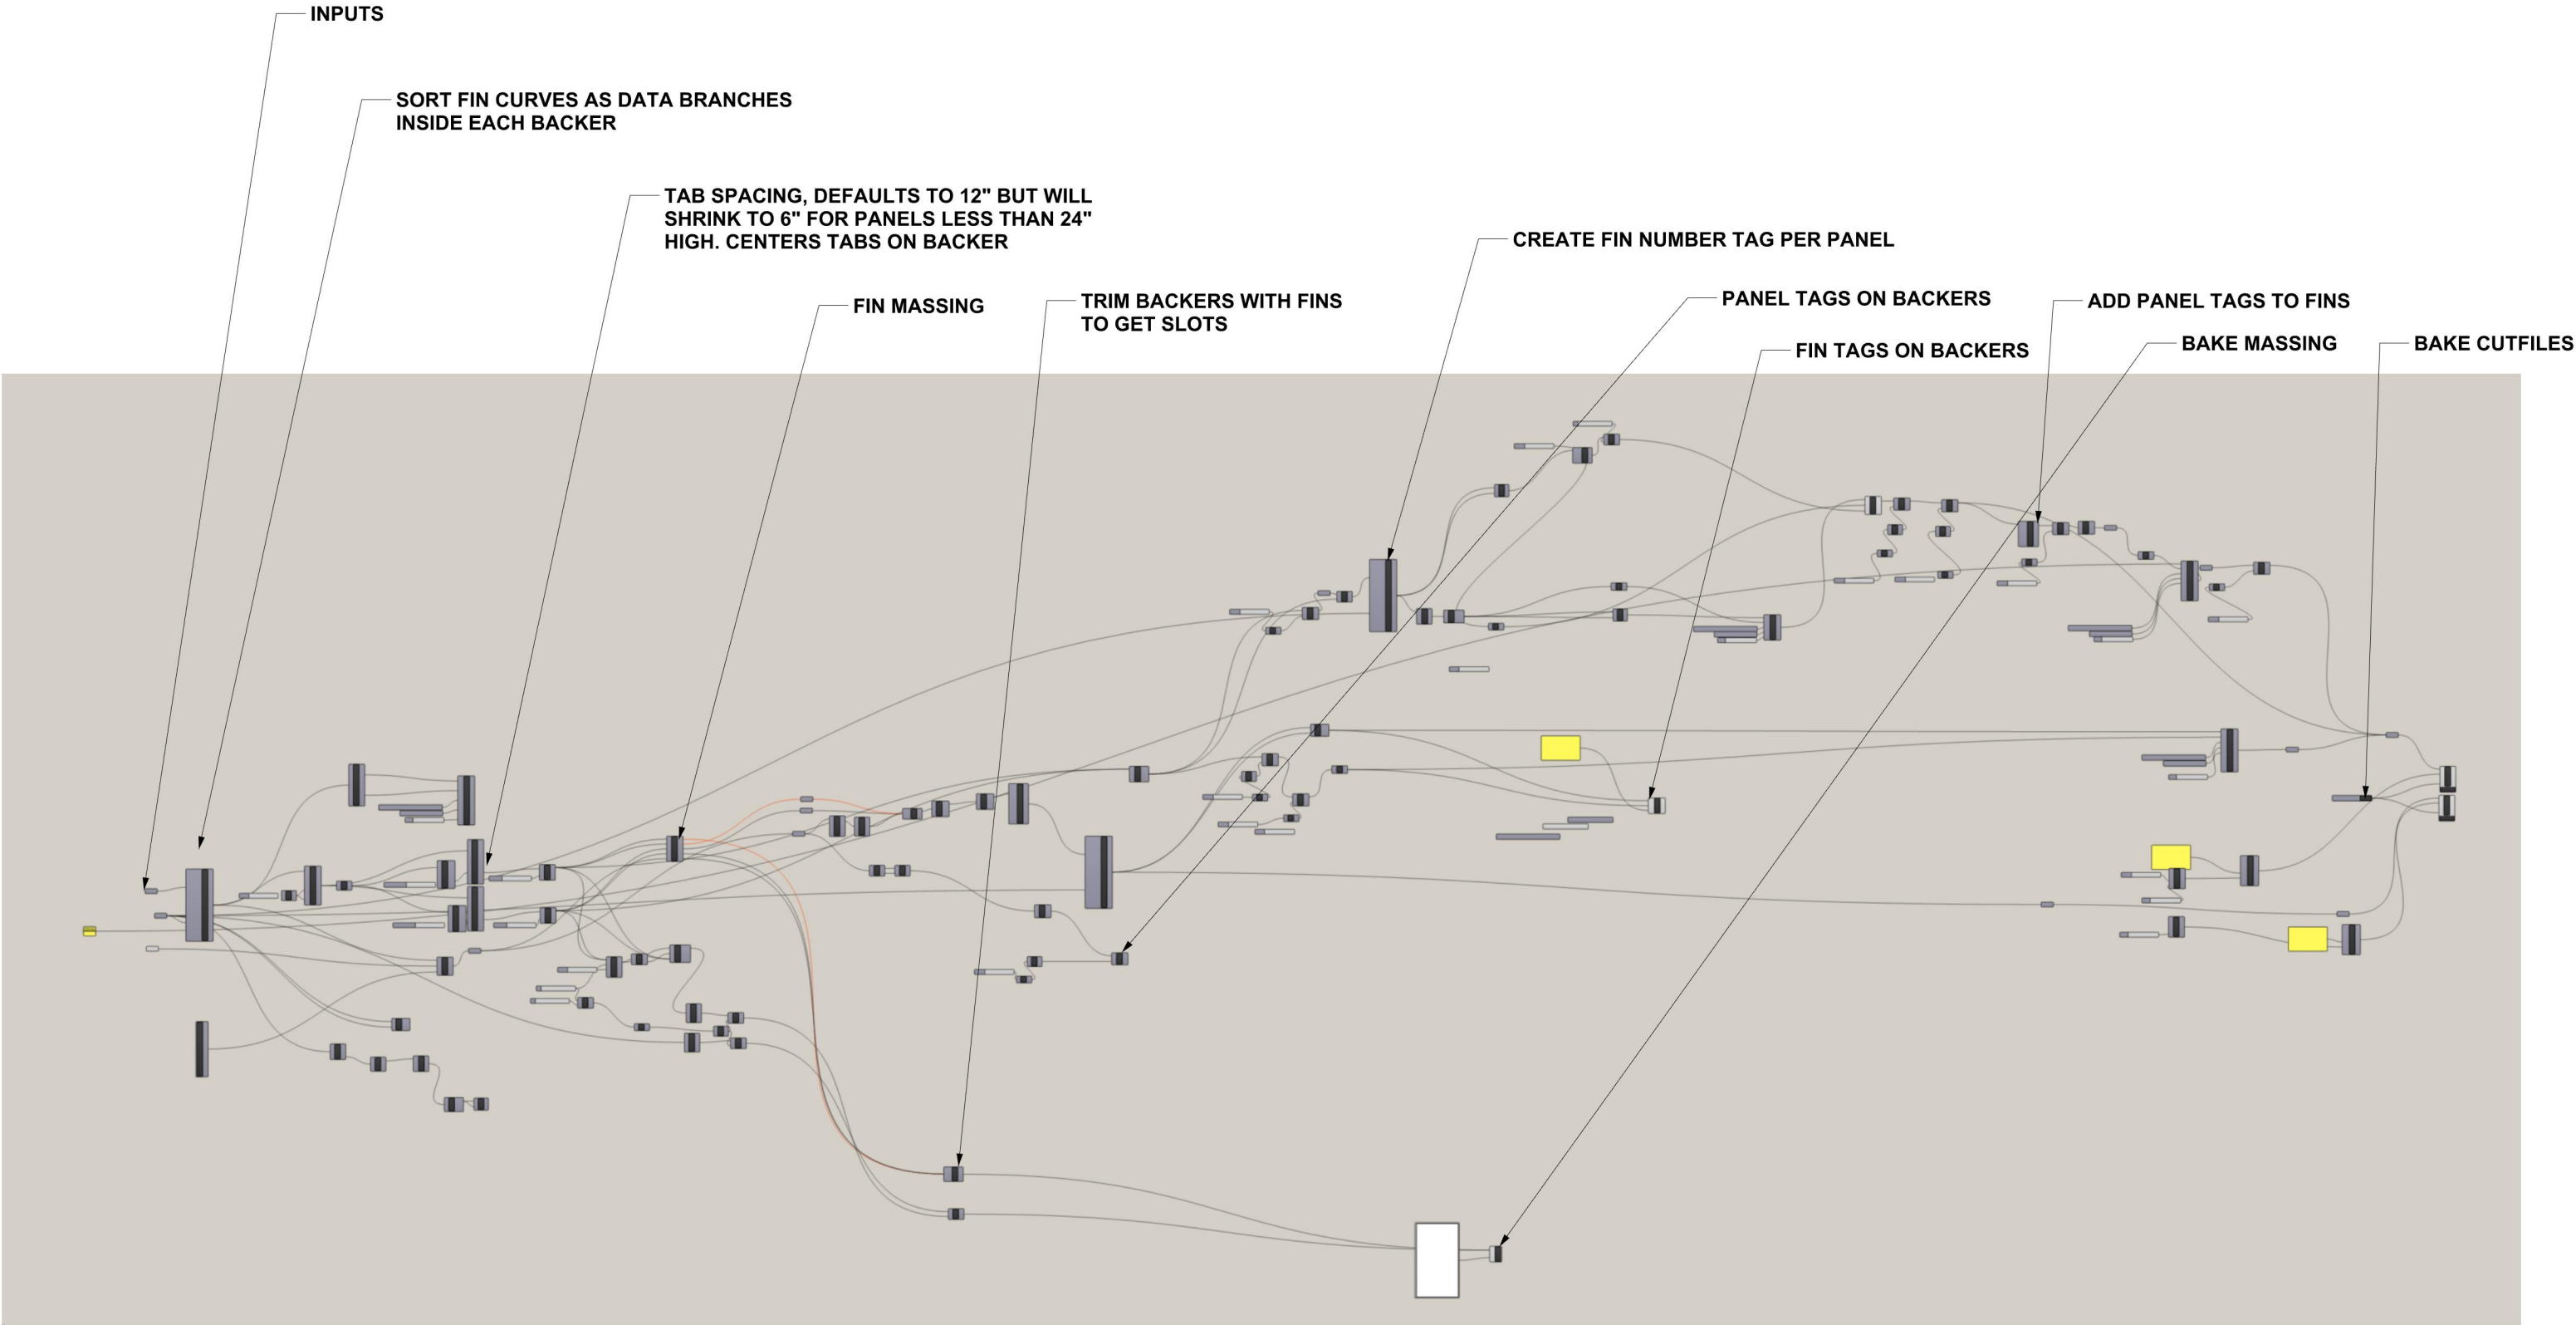

CONTOUR WALL, FLOW NOTATION (IN PROGRESS)
NTS


The turf color badge project is an ongoing initiative to make desk objects for our staff every Wednesday. I have been the designer most of the weeks and have instructed others in the parameters. Cut file time, assembly time and concept are all driving factors of a good badge.

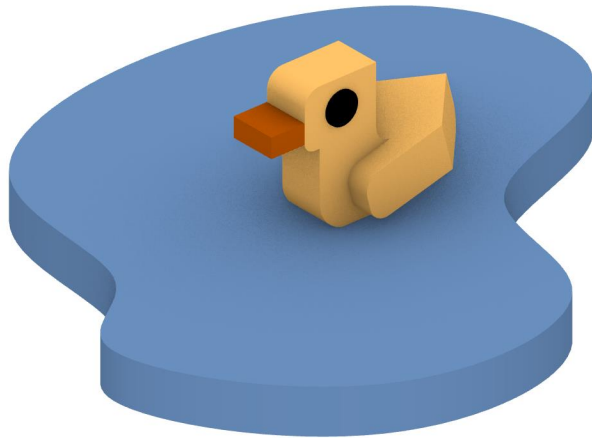

31 AZURE

NTS

10

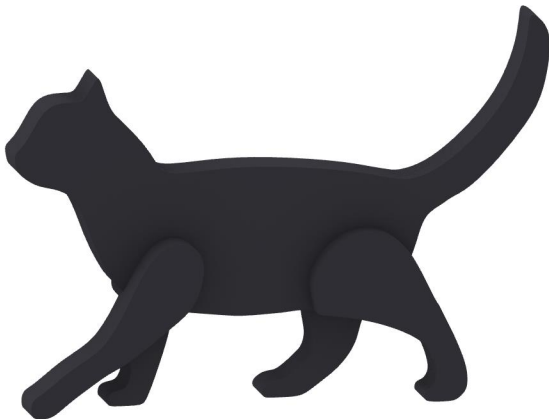

07 BLACK

NTS


08



06 CHARCOAL

NTS


06

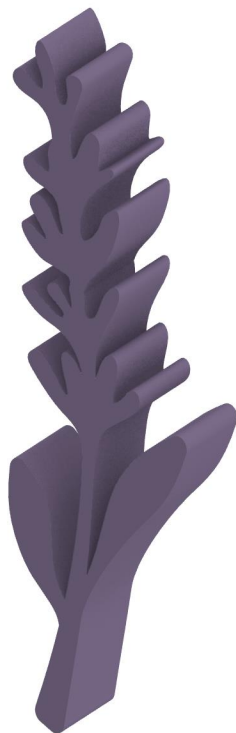

41 DRIED LAVENDER

NTS


04

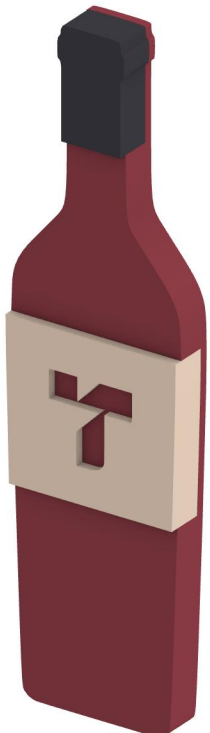

15 MERLOT

NTS


02

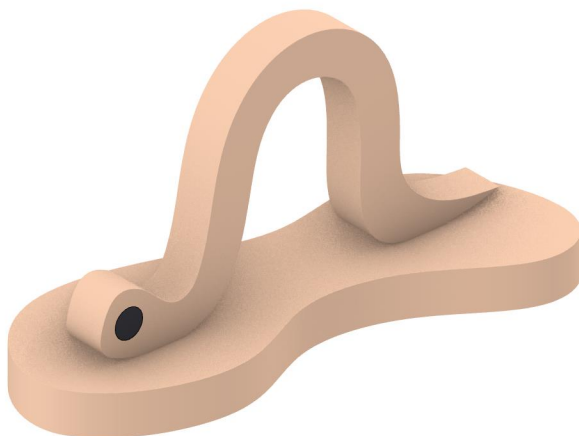

82 BARLEY

NTS

09

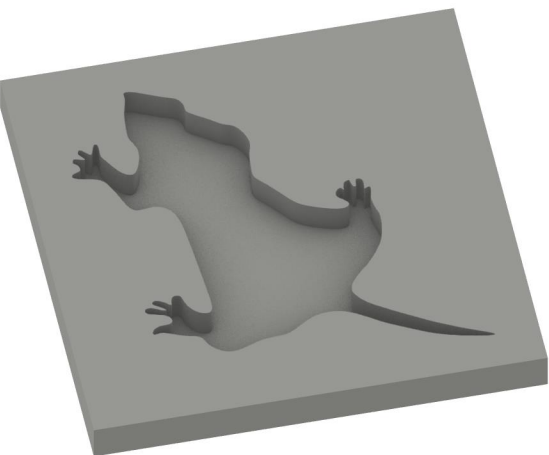

11 CELADON

NTS


07



27 JEAN JACKET

NTS

05

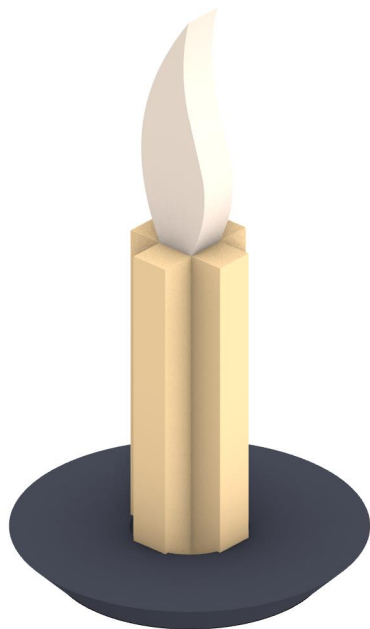

33 LUMINARY

NTS


03



83 HOLLAND OATS

NTS

01

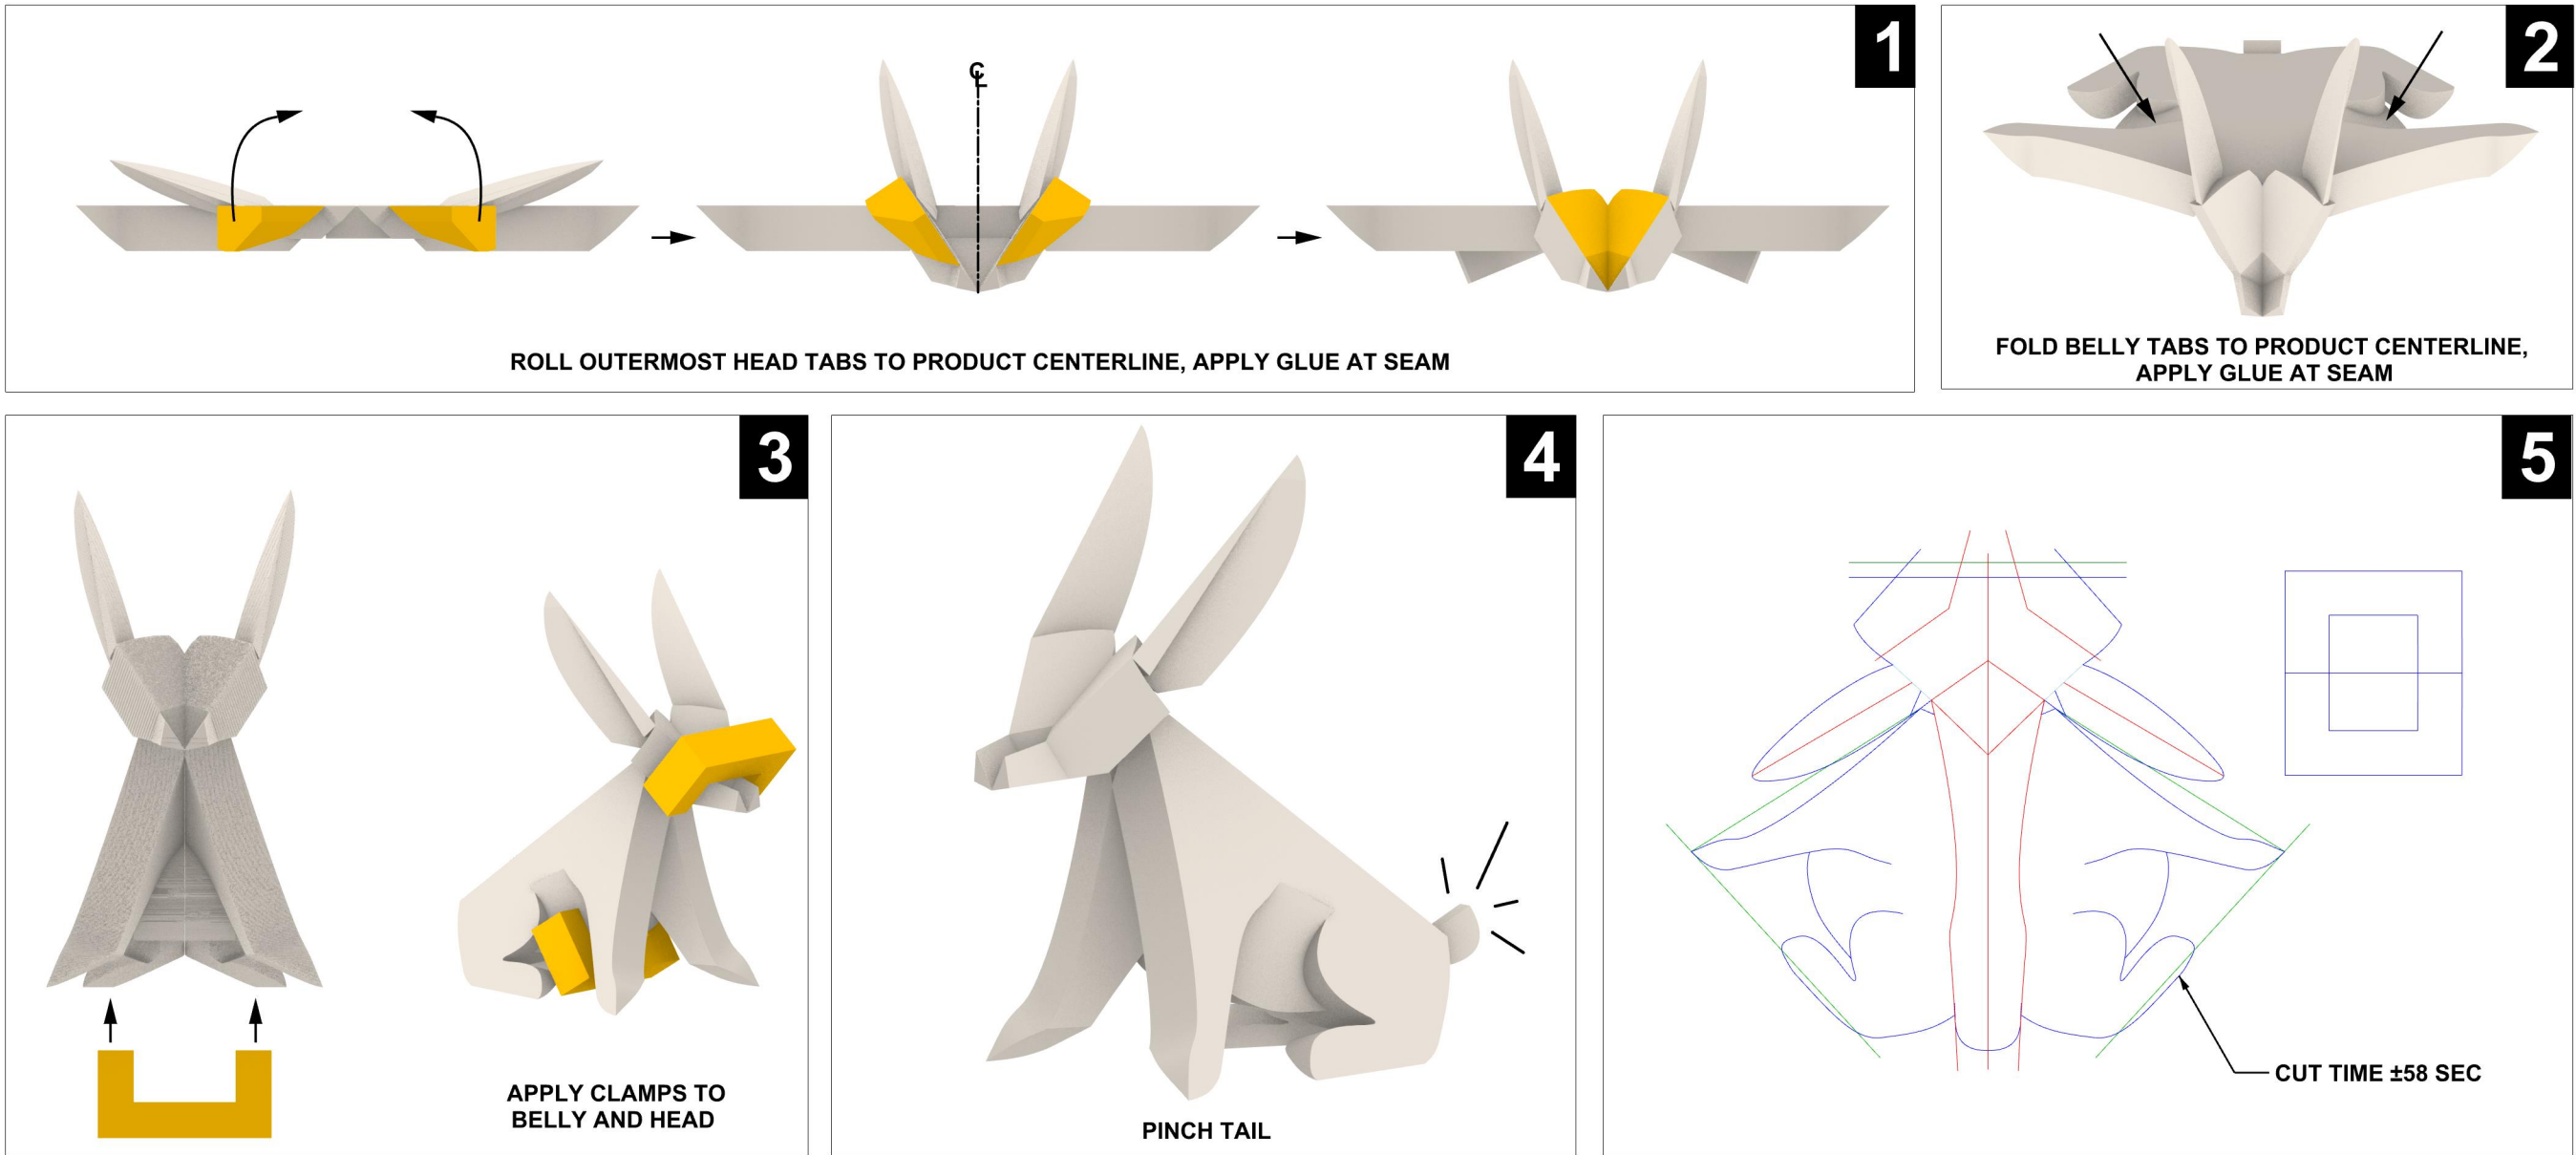



TURF BUNNY
NTS 01

STONE TEXTURE SAMPLE BOX

01


NTS

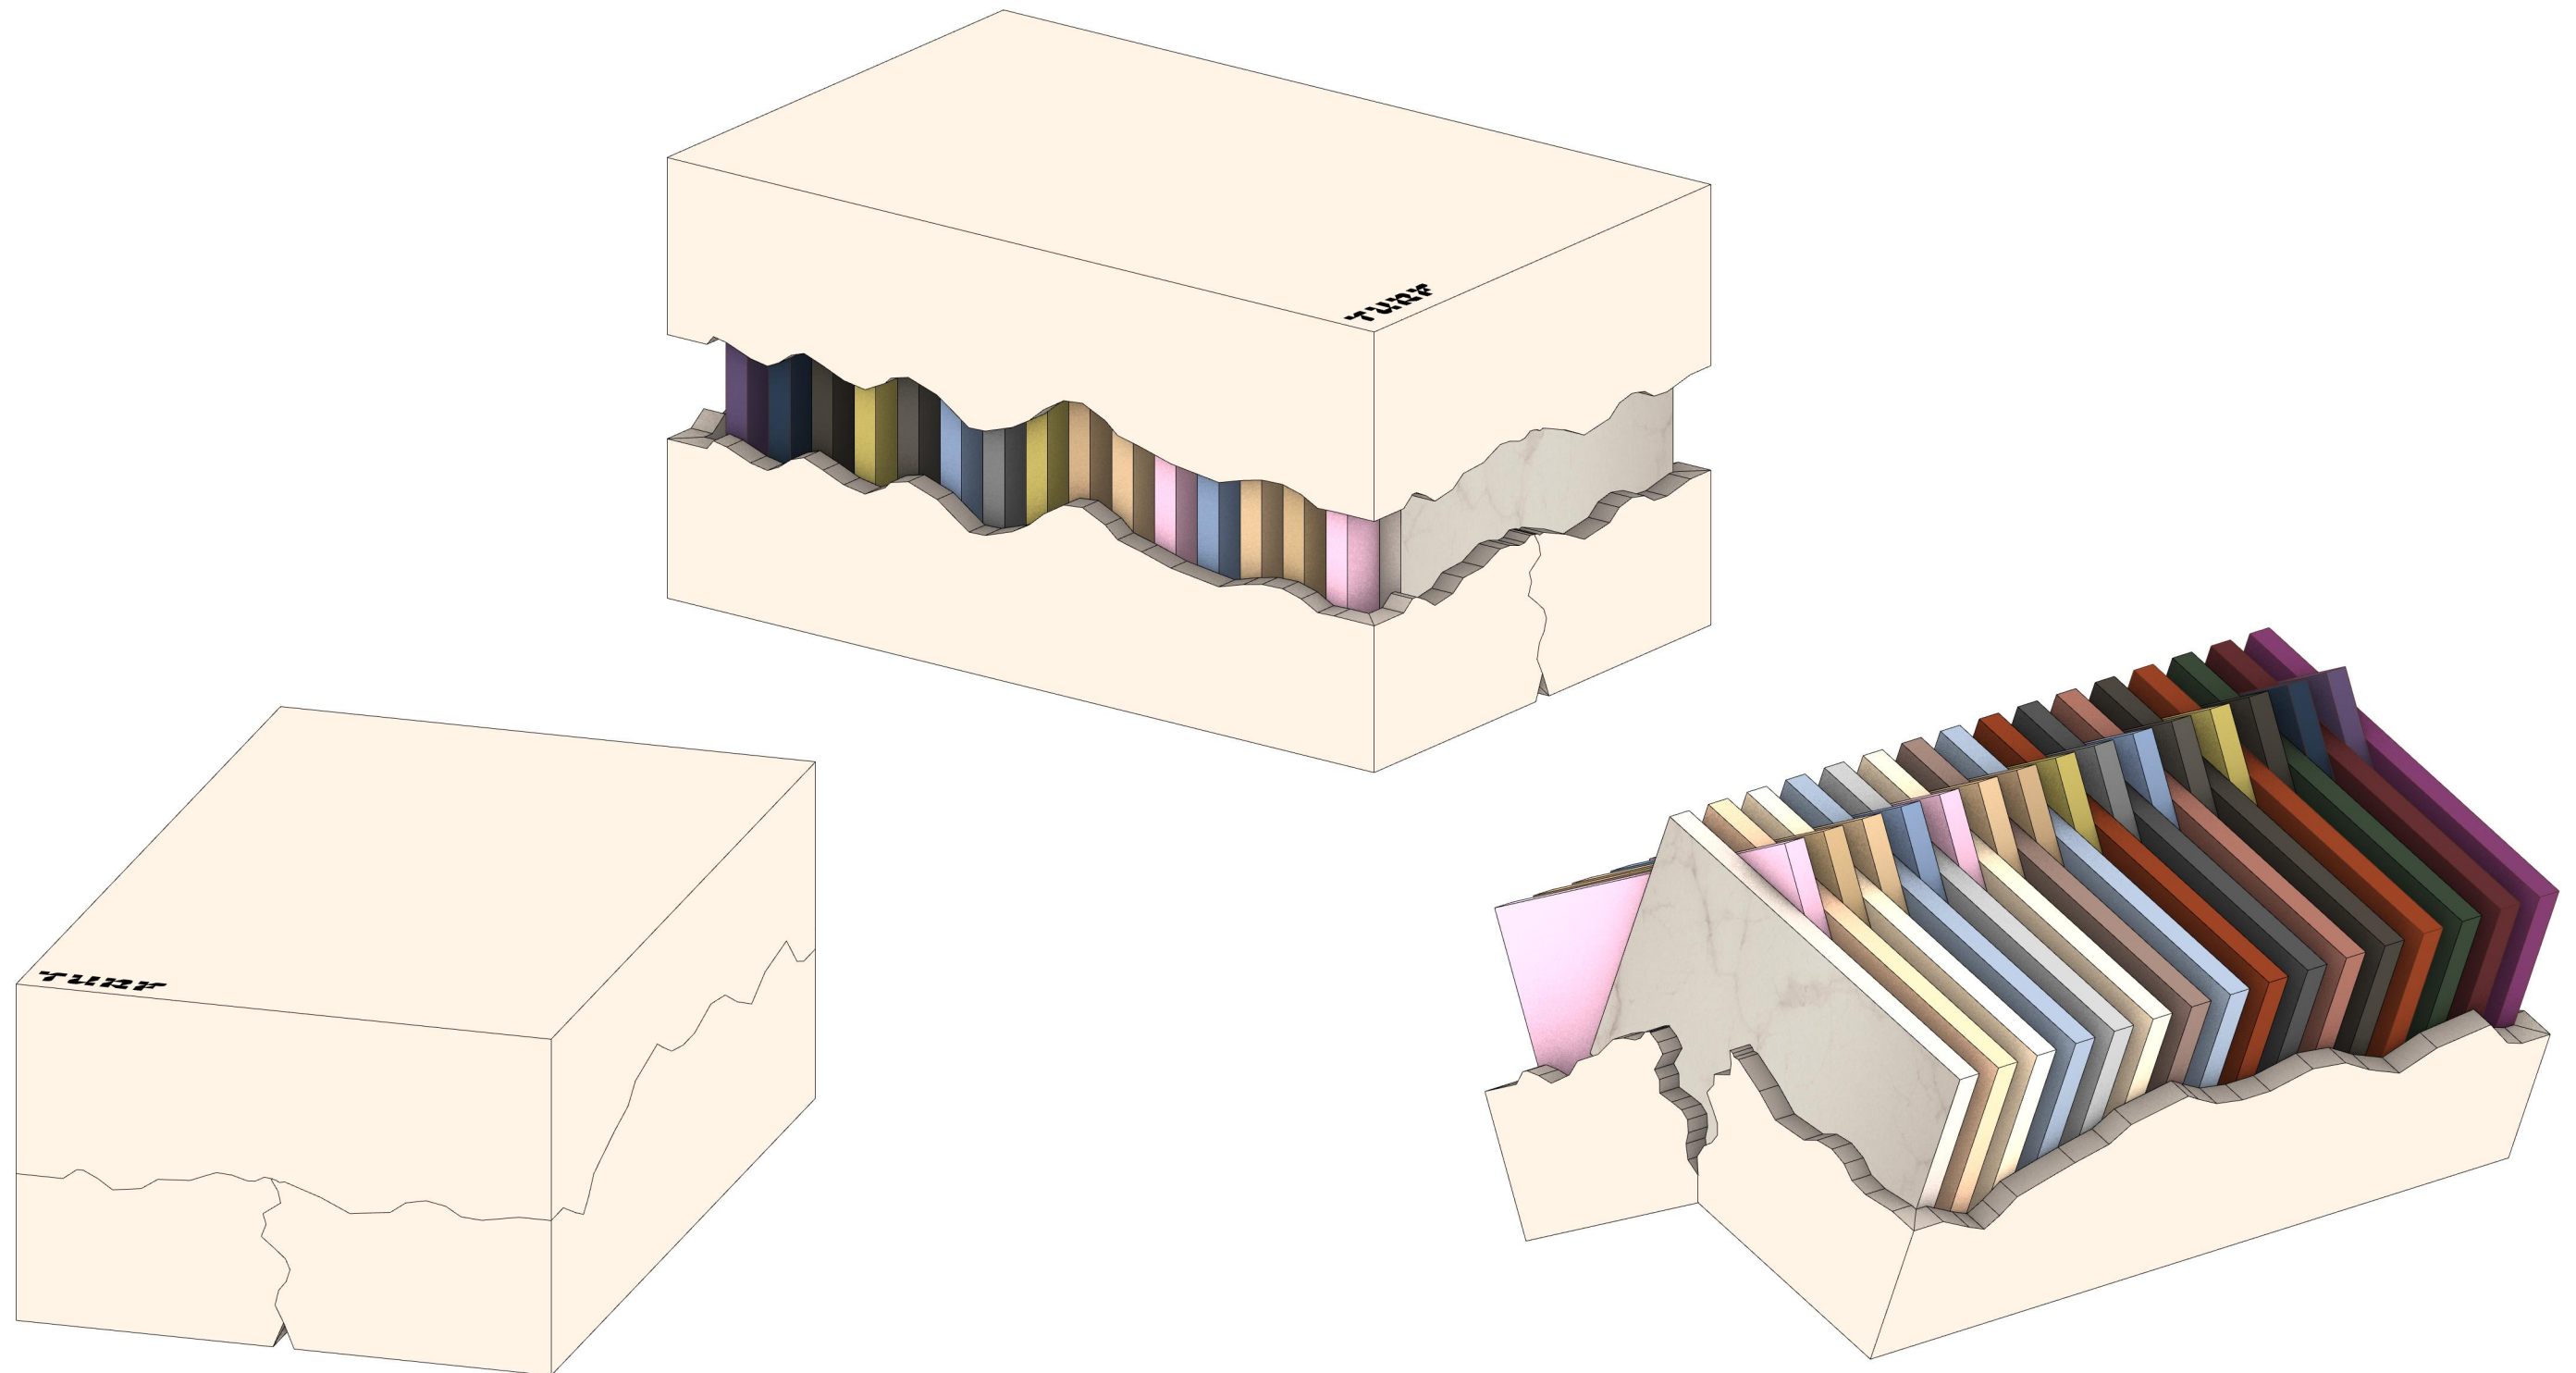

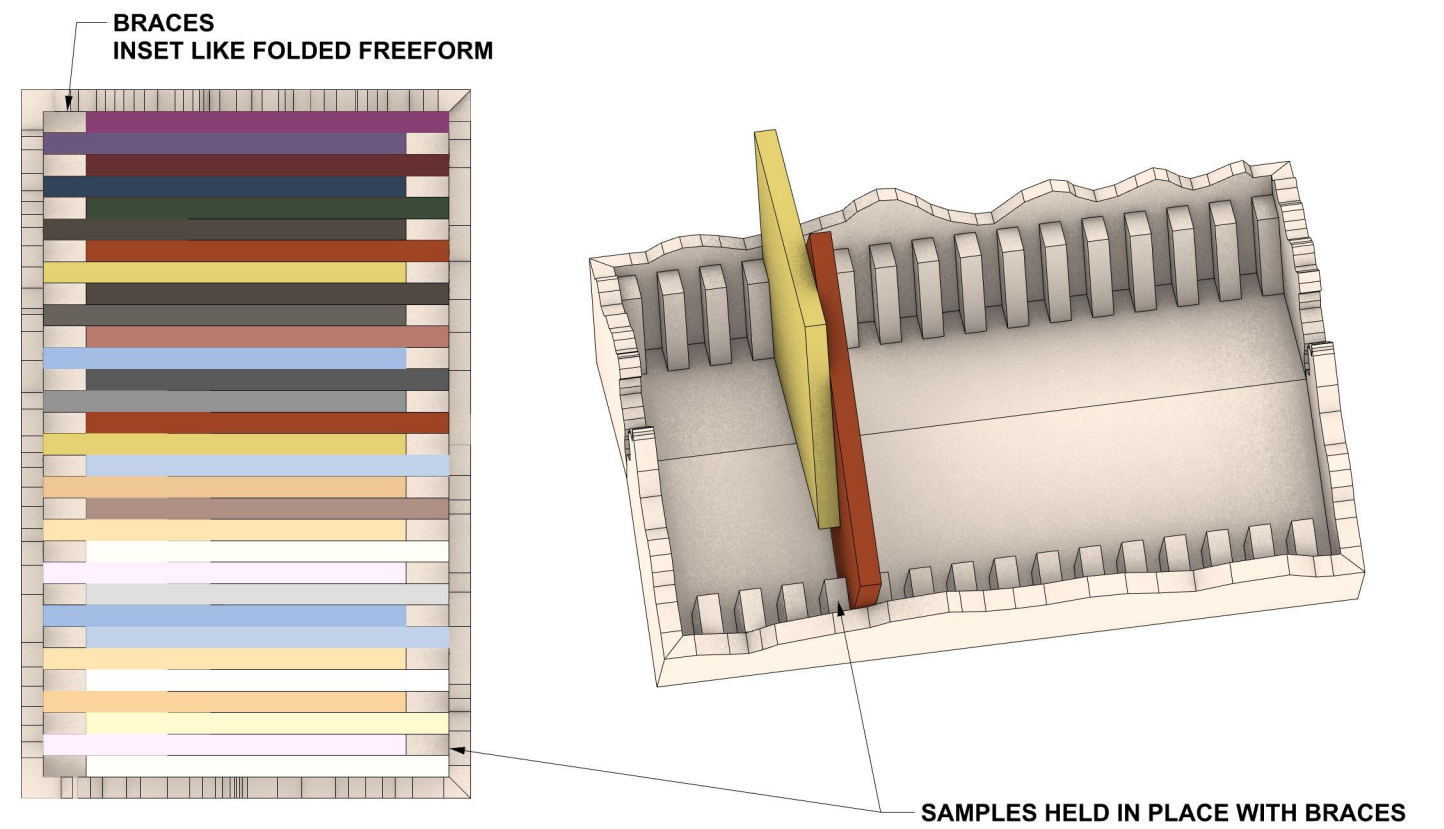

STONE TEXTURE SAMPLE BOX - FRICTION FIT

02
NTS

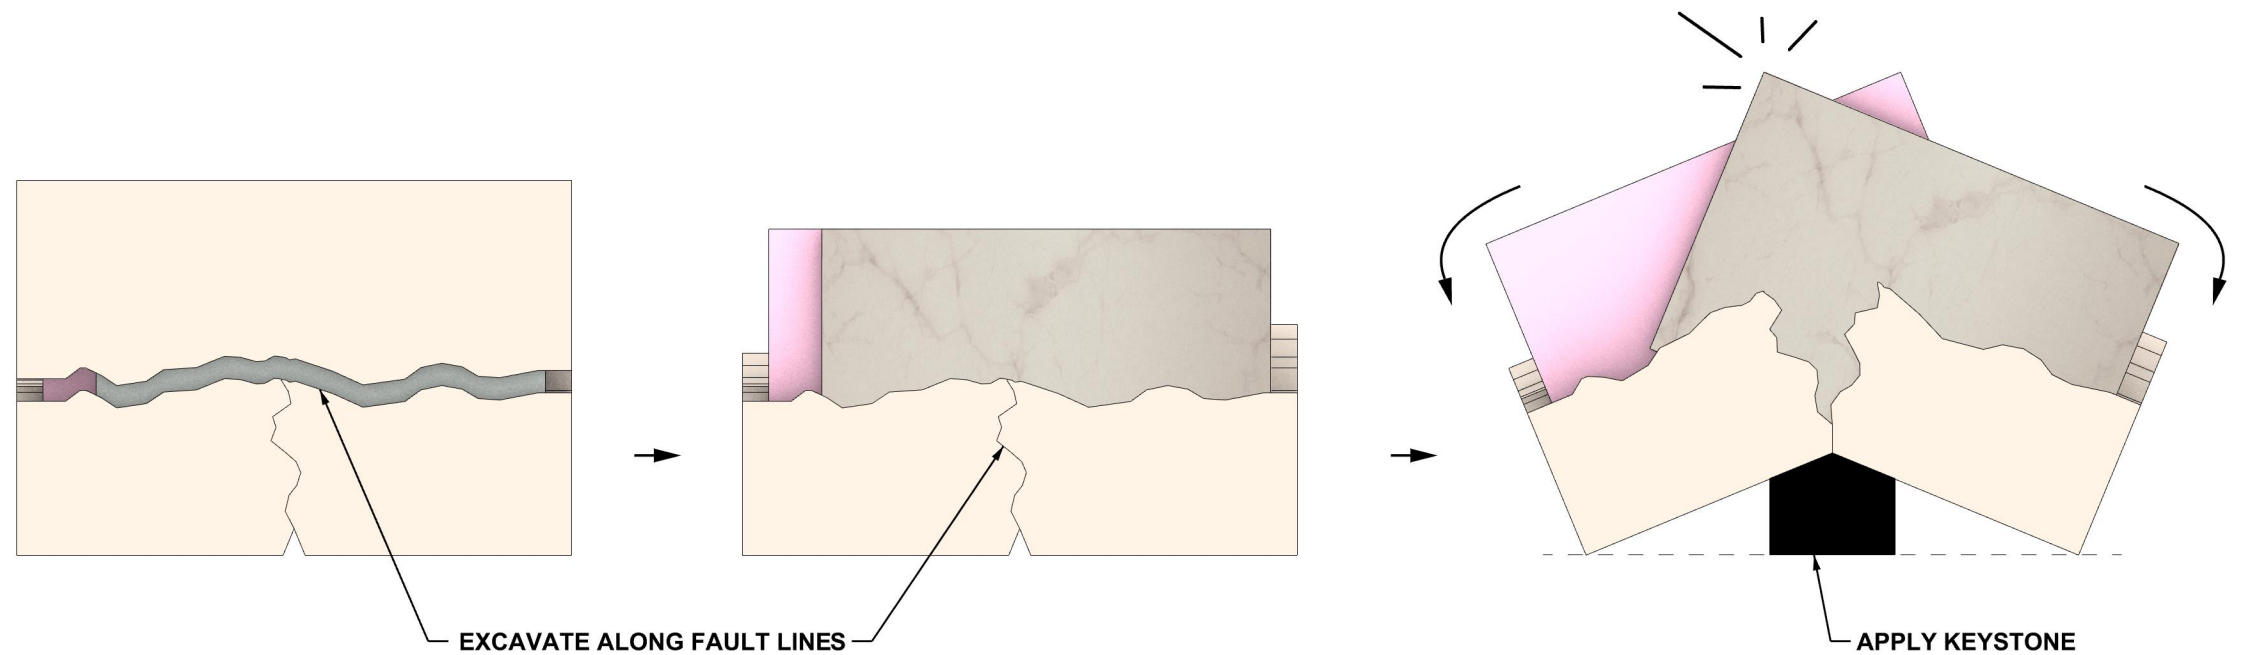


STONE TEXTURE SAMPLE BOX - EXCAVATION SEQUENCE

01
NTS


FRUIT



PICNIC BASKET
NTS 04

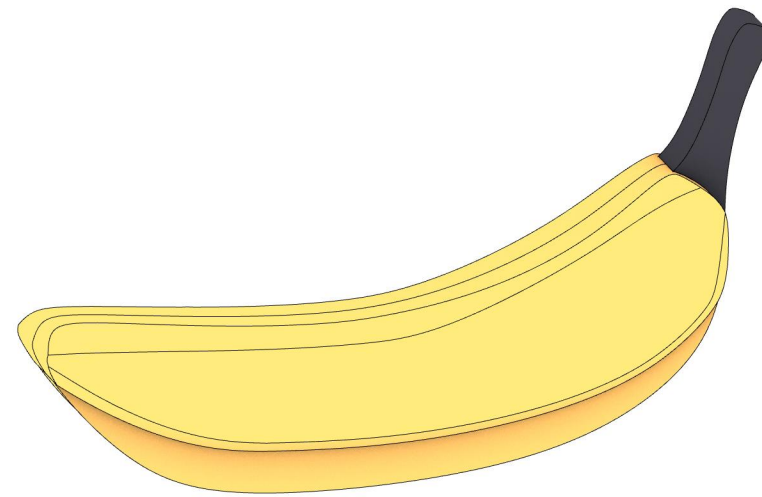

BANANA
NTS 03

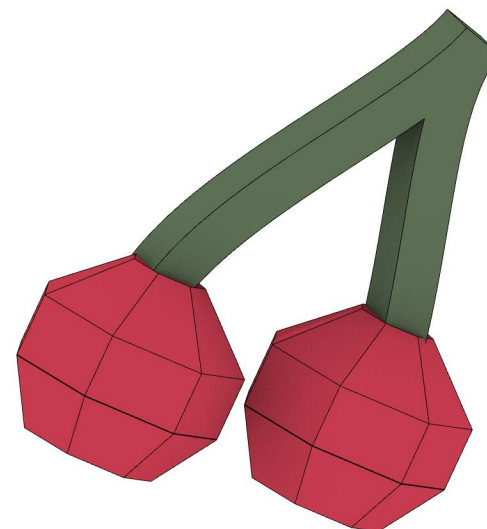

CHERRIES
NTS 02



PINEAPPLE
NTS 01